BARRIO GASPAR GIAI

Este proyecto de barrio social integra conceptos de sostenibilidad, espacios compartidos y atractivo visual a través de una estructura central innovadora y de edificios complementarios diseñados para fomentar la convivencia. La disposición en hexágono central alberga una cascada funcional, resaltando la relación simbiótica entre arquitectura y naturaleza.

IMAGEN SATELITAL DEL SITIO

La arquitectura se destaca por sus formas curvas, reflejando un enfoque contemporáneo y orgánico. Los caminos y áreas de juego siguen líneas sinuosas, generando un flujo natural dentro del barrio que contrasta con la estructura hexagonal central, creando armonía entre lo geométrico y lo orgánico.

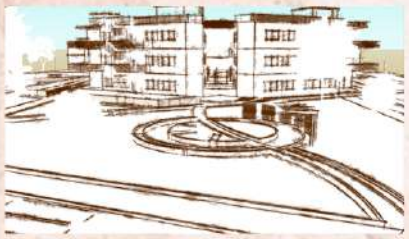

PLANTAS BAJAS Y VISTAS
CORRESPONDIENTES A AMBOS EDIFICIOS

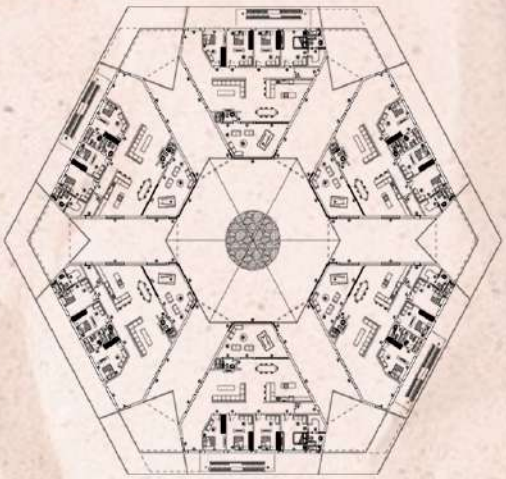

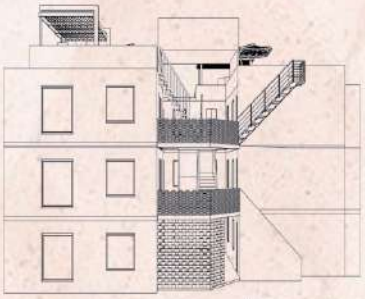

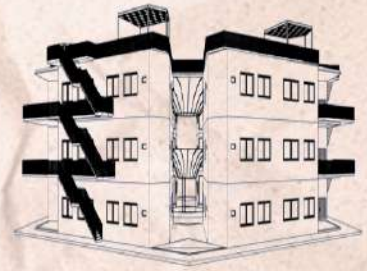

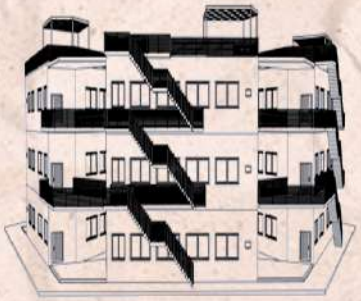

PLANTA GENERAL AL ESTILOCROQUIS

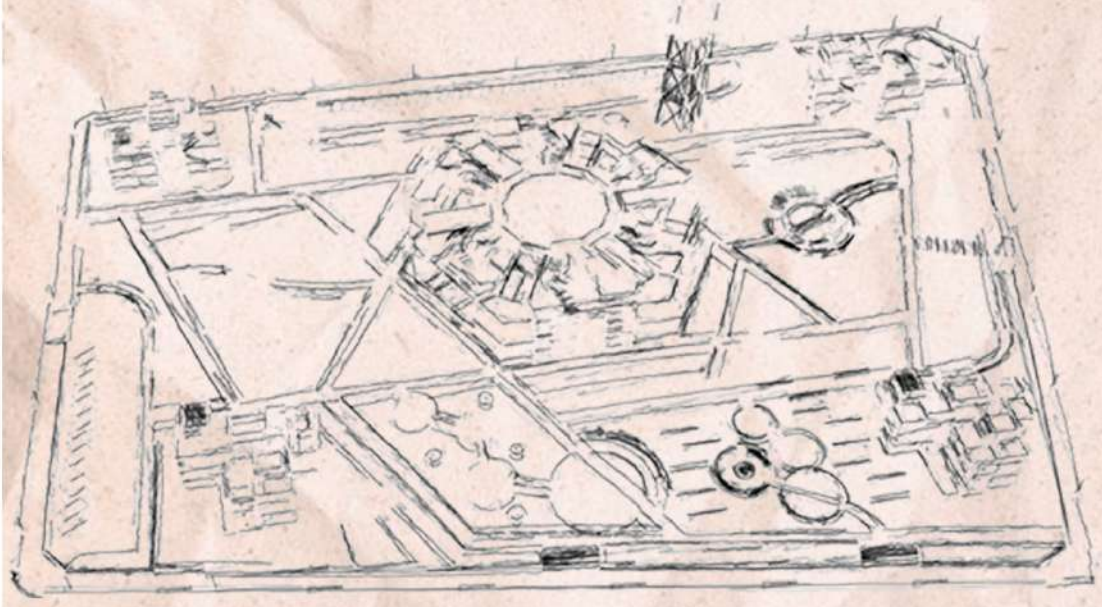

IMAGEN RENDERIZADA DE LA
ESTRUCTURA DENTRO DEL EXAGONO

IMAGEN RENDERIZADA DE LA ZONA
OESTE DEL BARRIO

URBANISMO

ESC. 1:380

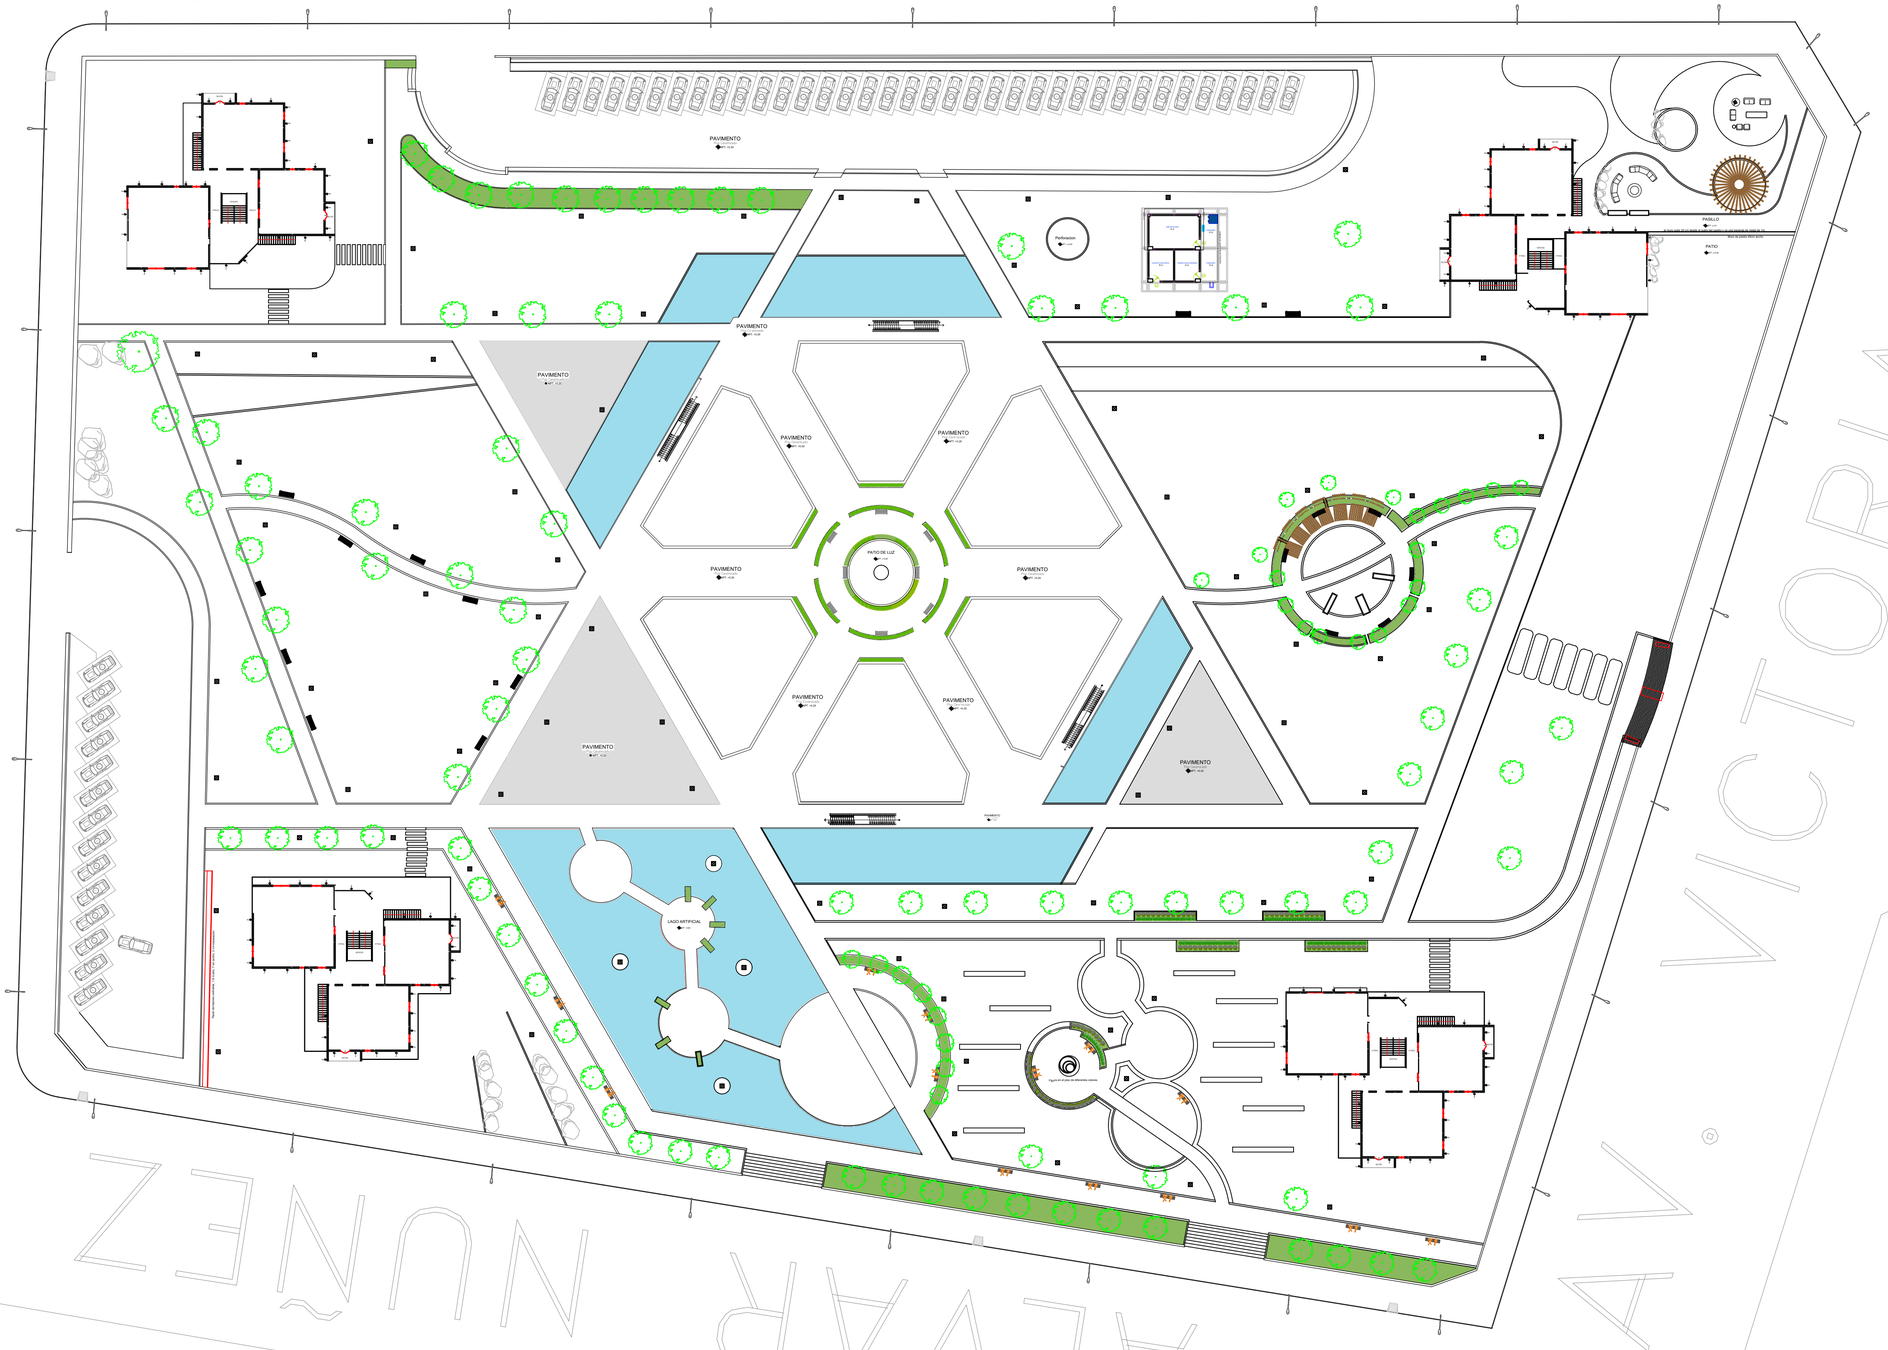
PAVIMENTO
PAVIMENTO
PAVIMENTO

PROTOTIPO 1

ESC. 1:100

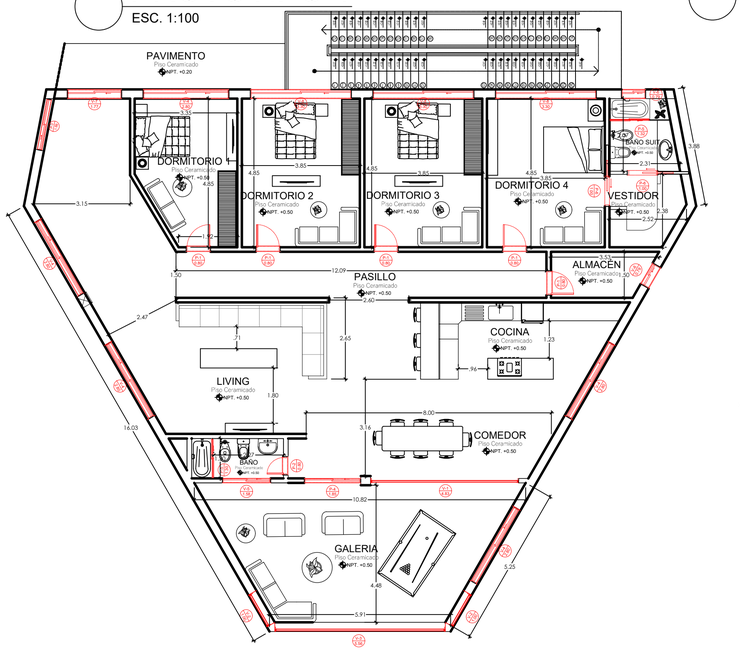

PLANTA BAJA EDIFICIO SECUNDARIO

ESC. 1:100

EDIFICIOS SOCIALES

100 m2

80 m2

64 m2

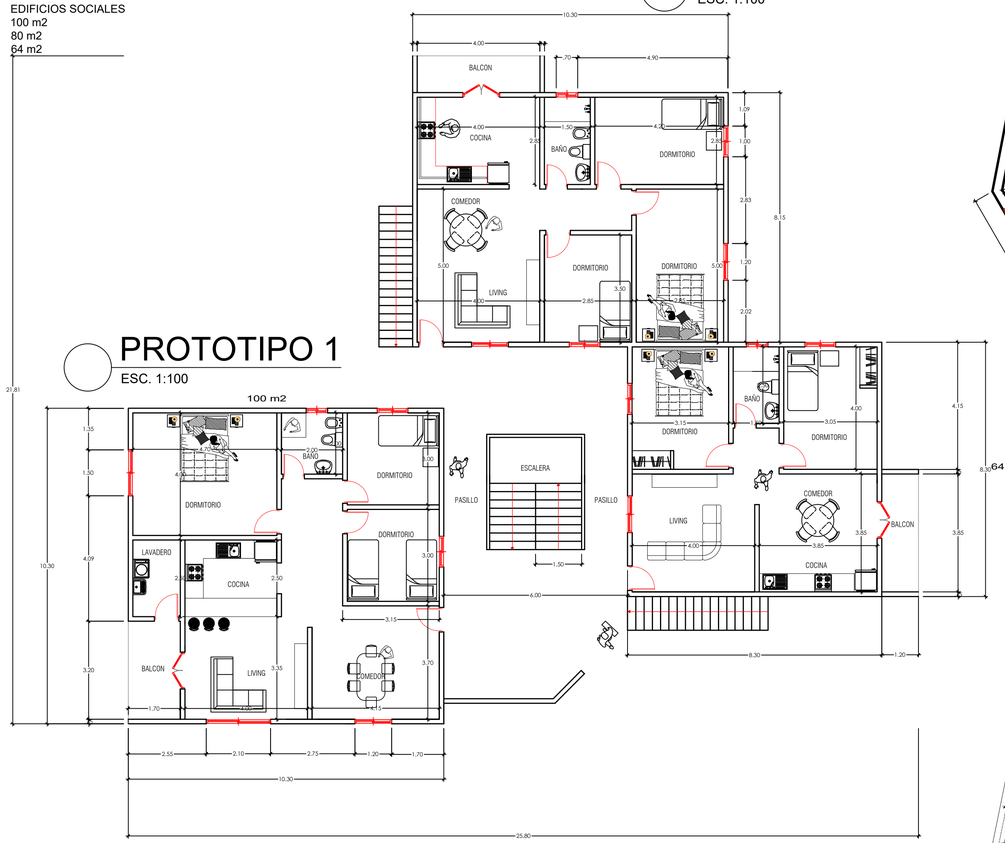

PROTOTIPO 2

ESC. 1:100

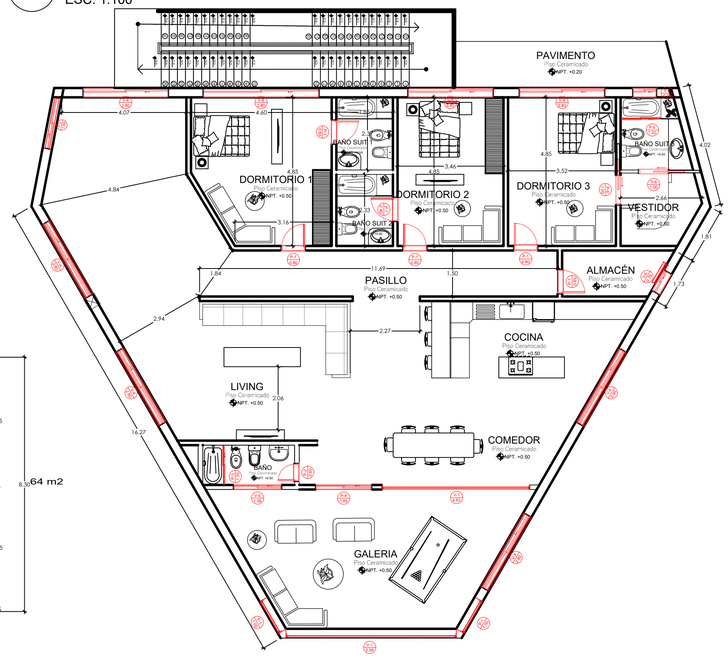

EDIFICIO-PRINCIPAL

VIGAS 1

ESC. 1:100

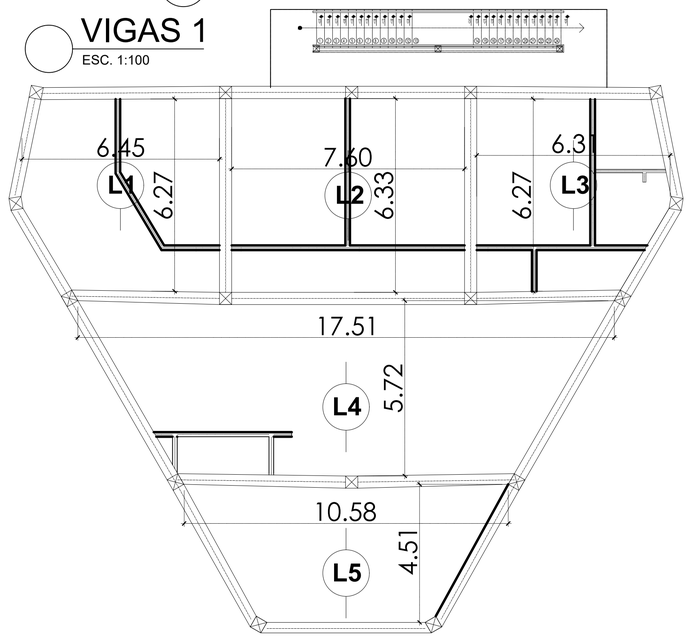

CORTE TRANSVERSAL EDIFICIO SECUNDARIO

ESC. 1:100

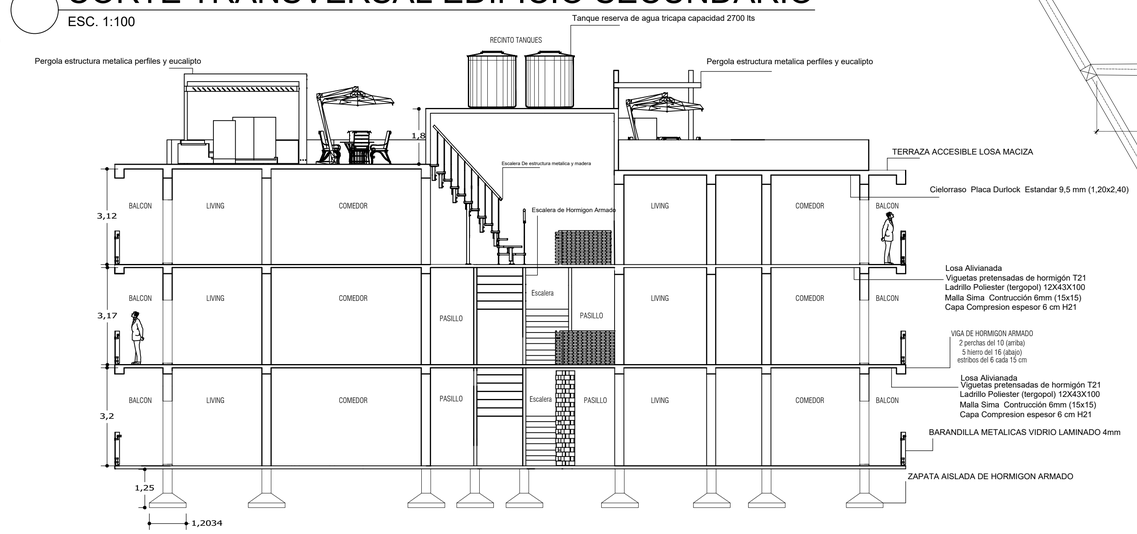

VIGAS 2

ESC. 1:100

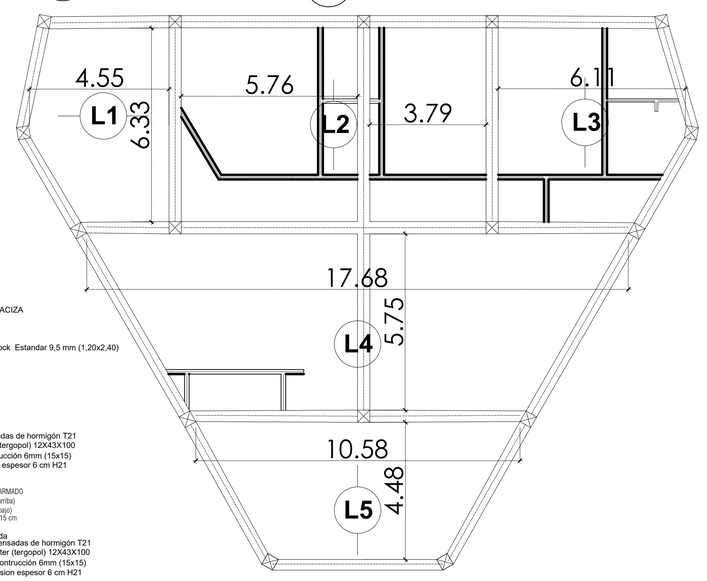

EDIFICIO-PRINCIPAL

Escuela Provincial Educación Técnica N°4 O.E.A		Materia: Proyecto IV	6 Año A Maestro Mayor de Obra	**Proyecto: Edificios sociales e intervención urbana, Andres Gaspar Giai**
Profesor Asesor: Gustavo Yanssen		Equipo de Proyecto:	Amarilla Carlos, Antunez Gonzalo, Barrios Alan y Beling Alexander	Titulo lamina: Departamentos de edificio principal y secundario
Fecha de inicio: 8/10/24	Fecha de finalización: 13/11/24	Fecha de presentación al publico: 14/11/24	Fecha de relevamiento: 1/10/24	Numero lamina: 2

FUNDACIONES 1

ESC. 1:100

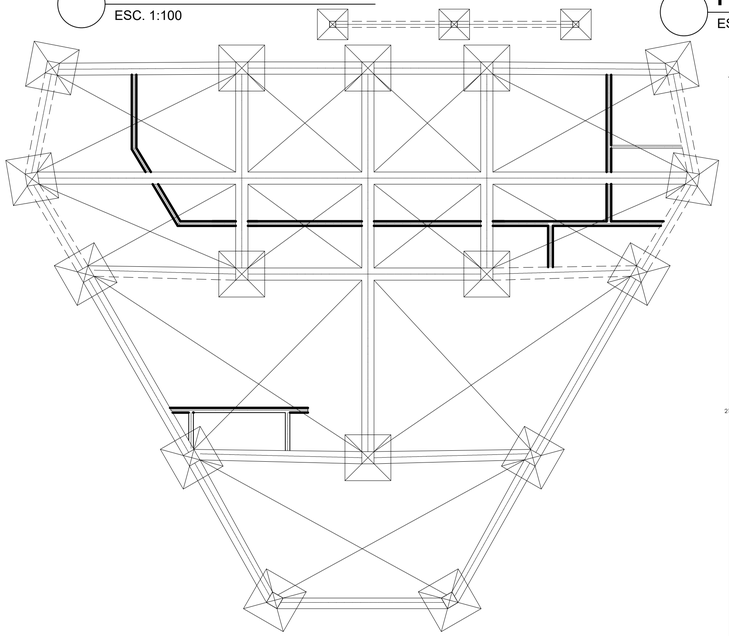

PLANTA 1ER PISO EDIFICIO SECUNDARIO

ESC. 1:100

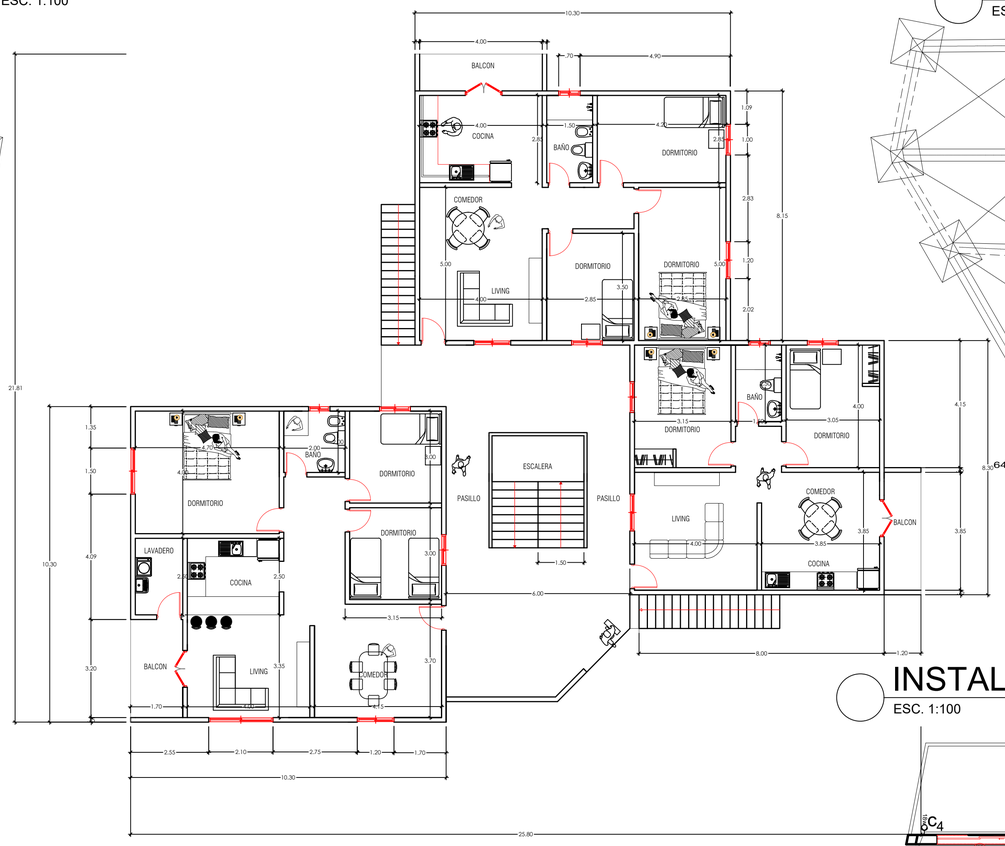

FUNDACIONES 2

ESC. 1:100

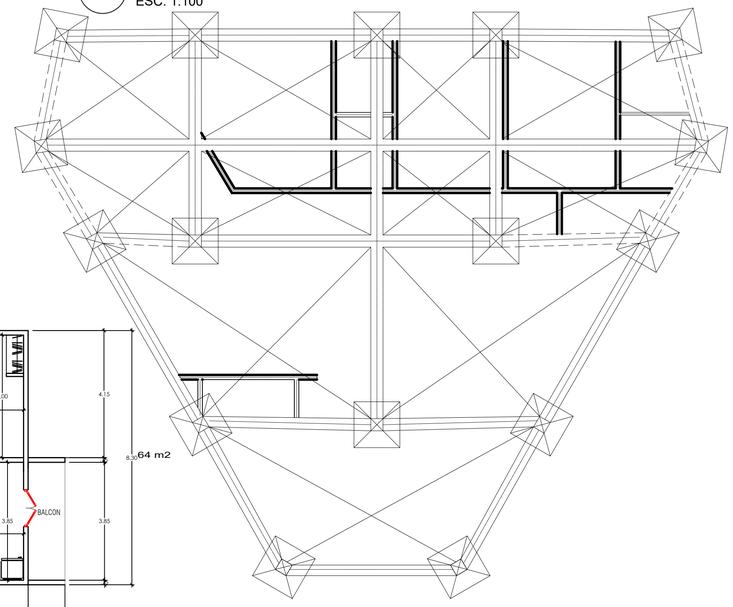

INSTALACIONES ELECTRICAS 1

ESC. 1:100

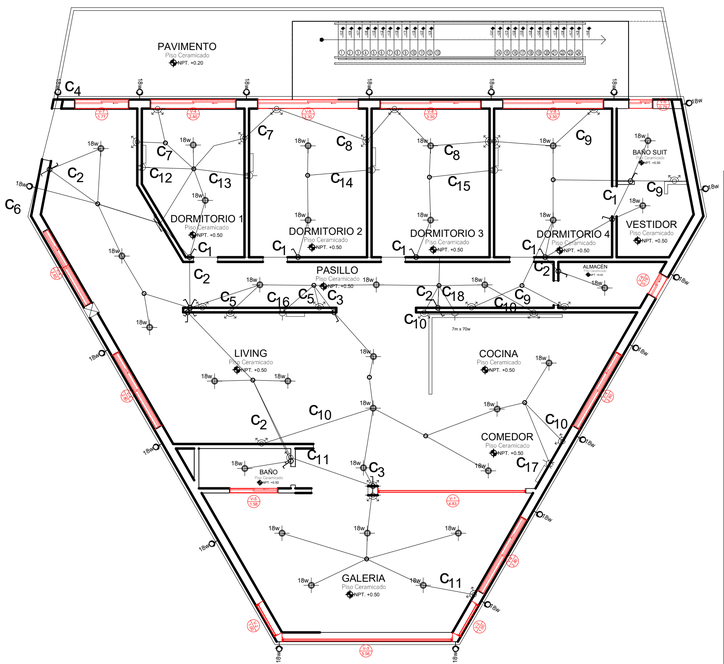

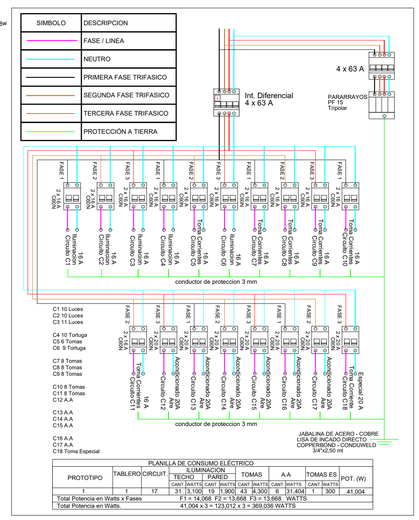

PLANILLA DE CONSUMO ELÉCTRICO													
PROTOTIPO	TABLERO	CIRCUIT.	ILUMINACION				TOMAS		A.A		TOMAS ES		POT. (W)
			TECHO		PARED								
			CANT.	WATTS	CANT.	WATTS	CANT.	WATTS	CANT.	WATTS	CANT.	WATTS	
1	1	17	31	3,100	19	1,900	43	8,300	6	31,404	1	300	41,004
Total Potencia en Watts x Fases			F1 = 14,068 F2 = 13,668 F3 = 13,668 WATTS										
Total Potencia en Watts.			41,004 x 3 = 123,012 x 3 = 369,036 WATTS										

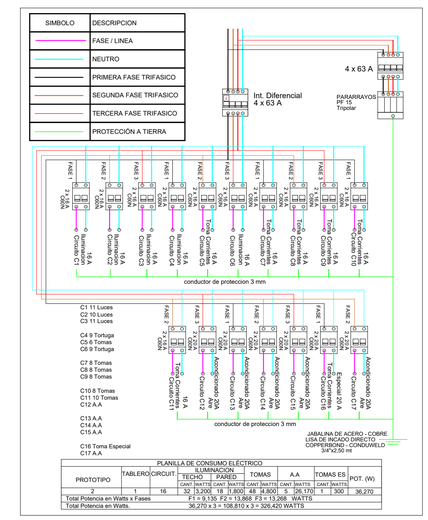

PLANILLA DE CONSUMO ELÉCTRICO													
PROTOTIPO	TABLERO	CIRCUIT.	ILUMINACION				TOMAS		A.A		TOMAS ES		POT. (W)
			TECHO		PARED								
			CANT.	WATTS	CANT.	WATTS	CANT.	WATTS	CANT.	WATTS	CANT.	WATTS	
2	1	16	32	3,200	18	1,800	48	14,800	5	26,170	1	300	36,270
Total Potencia en Watts x Fases			F1 = 9,135 F2 = 13,868 F3 = 13,268 WATTS										
Total Potencia en Watts.			36,270 x 3 = 108,810 x 3 = 326,420 WATTS										

Simbologia	Descripción	Altura m
18w	SALIDA DE ILUMINACIÓN EN TECHO	TECHO
18w	SALIDA DE ILUMINACIÓN EN PARED TIPO TORTUGA	TECHO
	TOMA CORRIENTES BIPOLAR DOBLE/CON LÍNEA A TIERRA, A PRUEBA DE HUMEDAD TOMA ATERRIZADA ISA 220V CON TAPA FRONTAL, GRADO DE PROTECCIÓN IP55	0.40
	TOMA CORRIENTES BIPOLAR CON LÍNEA A TIERRA, TOMA ATERRIZADA 20A APRUEBA DE HUMEDAD, TOMA ATERRIZADA 20A CON TAPA FRONTAL GRADO DE PROTECCIÓN IP55 SIMILAR	1
	INTERRUPTOR DE LUCES UNIPOLAR	1.20

	CONMUTADOR DE LUCES UNIPOLAR	1.20
	CAJA DE DISTRIBUCIÓN DIFERENCIAL PRINCIPAL	1.20
	CAJA OCTOGONAL CONTENEDOR ELÉCTRICO	TECHO
	AIRE ACONDICIONADO DE 4500 REFRIGERIOS	2.10
A A	TOMA CORRIENTES BIPOLAR CON LINEA A TIERRA, TOMA ATERRIZADA 20A A PRUEBA DE HUMEDAD, TOMA ATERRIZADA 20A CON TAPA FRONTAL GRADO DE PROTECCIÓN IP55 SIMILAR	2.10
m x 10w	Kit Manguera Luz Neon Fuente + Ficha Interior	2.10

INSTALACIONES ELECTRICAS 2

ESC. 1:100

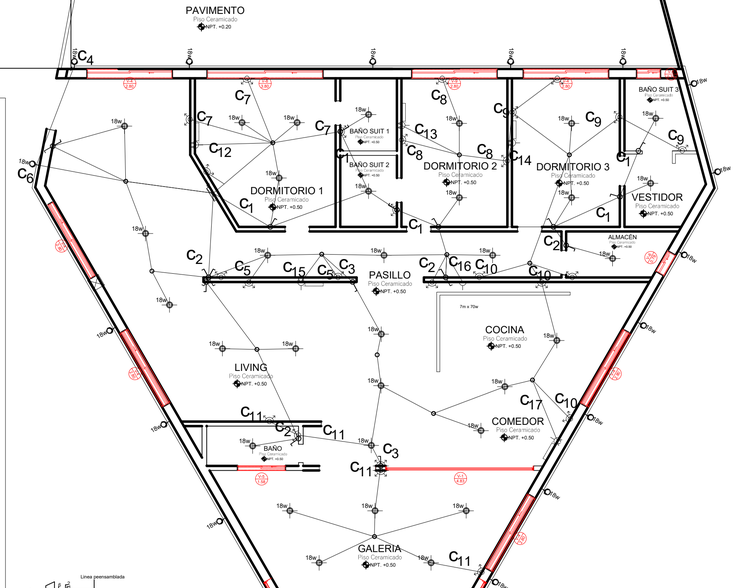

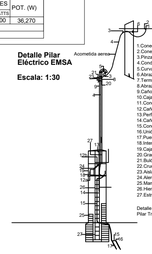

Escuela Provincial Educación Técnica N°4 O.E.A		Materia: Proyecto IV	6 Año A Maestro Mayor de Obra	**Proyecto: Edificios sociales e intervención urbana, Andres Gaspar Giai**
Profesor Asesor: Gustavo Yanssen		Equipo de Proyecto:	Amarilla Carlos, Antunez Gonzalo, Barrios Alan y Beling Alexander	Titulo lamina: Replanteo e Instalaciones eléctricas
Fecha de inicio: 8/10/24	Fecha de finalización: 13/11/24	Fecha de presentación al publico: 14/11/24	Fecha de relevamiento: 1/10/24	Numero lamina: 3

INSTALACIONES SANITARIAS 1

ESC. 1:100

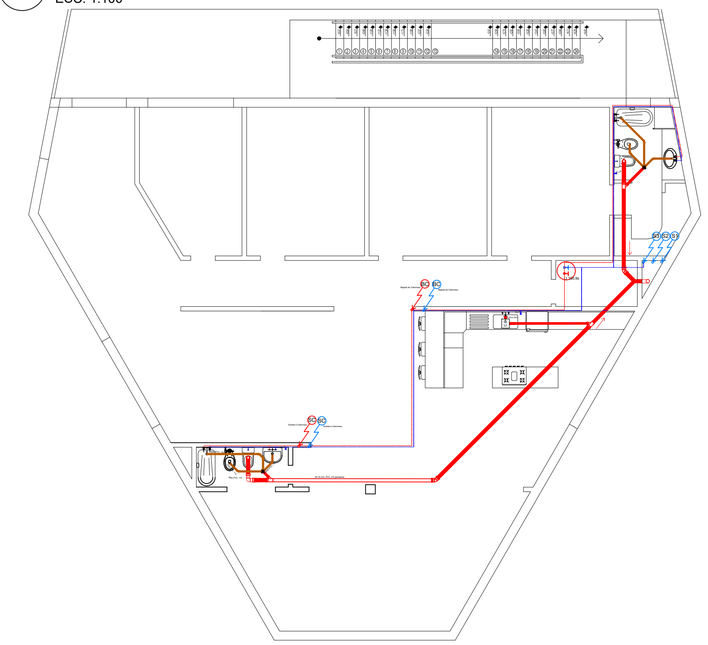

PLANTA 2DO PISO EDIFICIO SECUNDARIO

ESC. 1:100

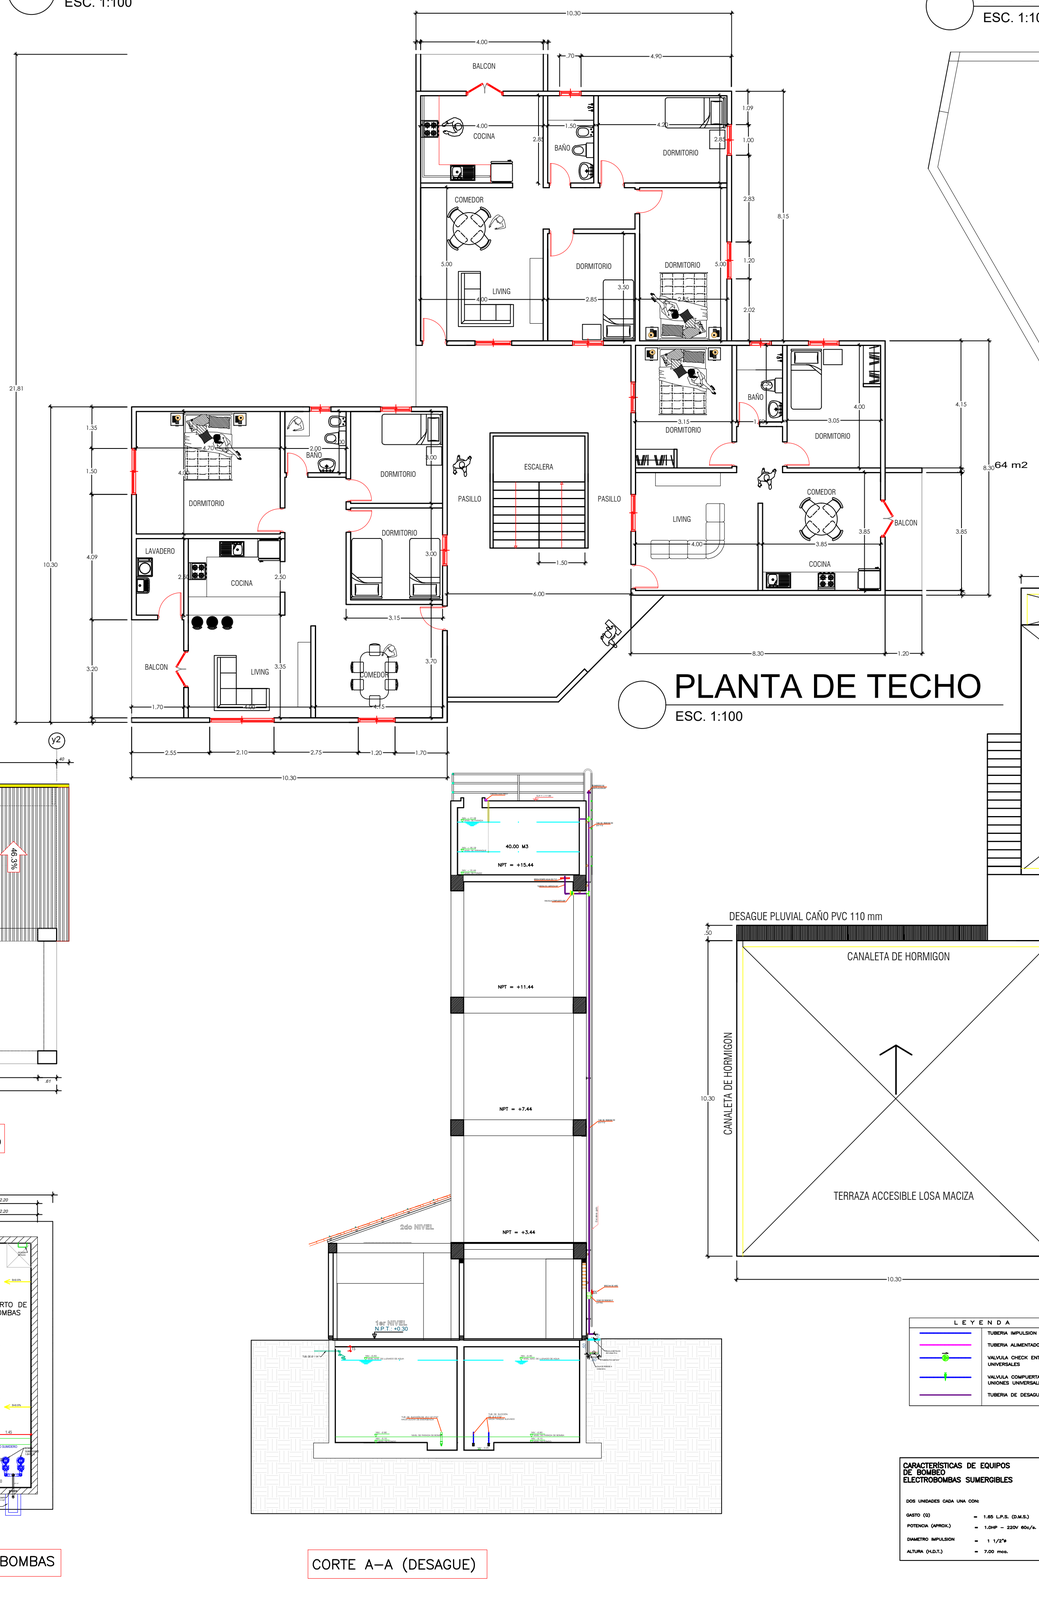

INSTALACIONES SANITARIAS 2

ESC. 1:100

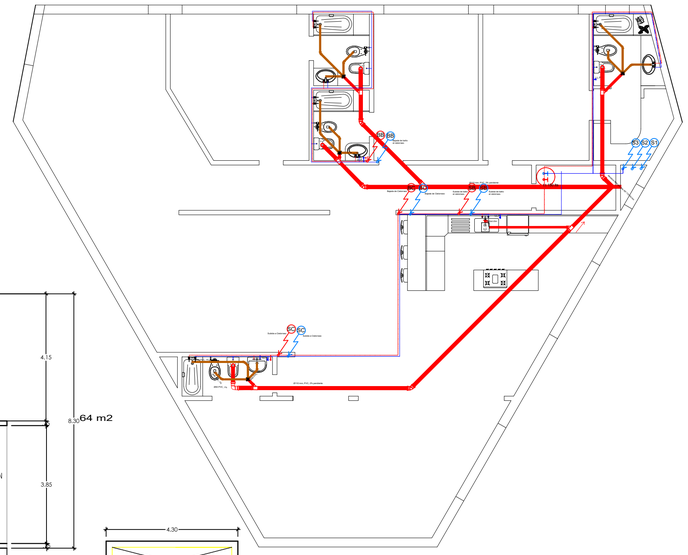

PLANTA DE TECHO

ESC. 1:100

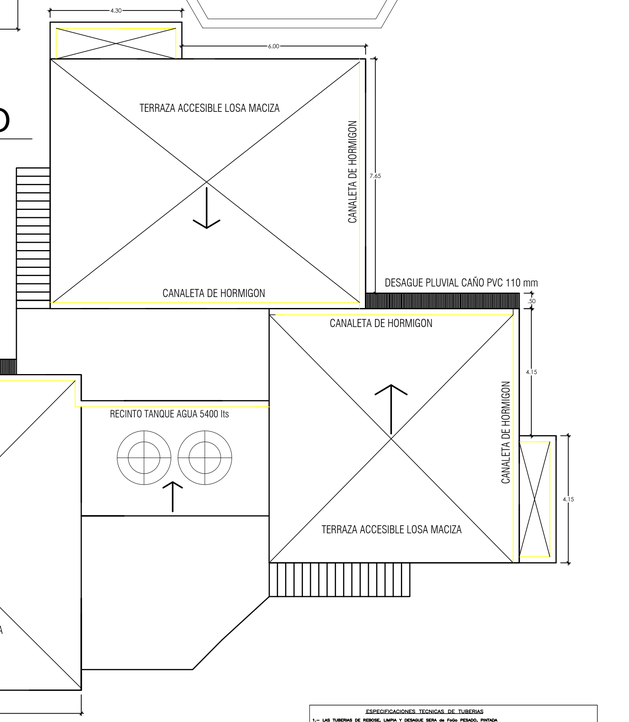

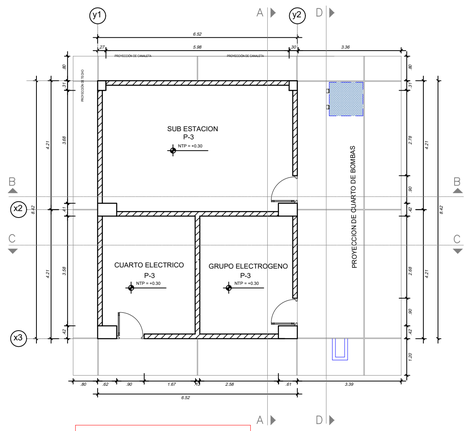

PLANTA PRIMER PISO

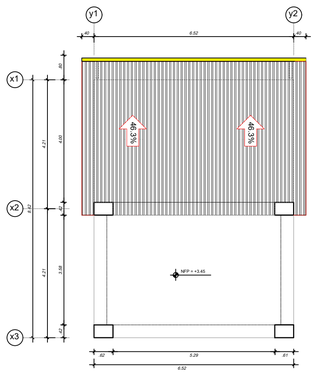

PLANTA SEGUNDO PISO

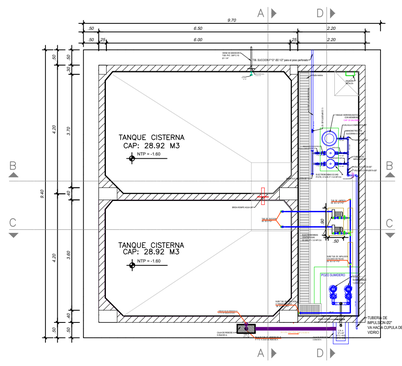

PLANTA CISTERNA – SISTEMA DE BOMBAS

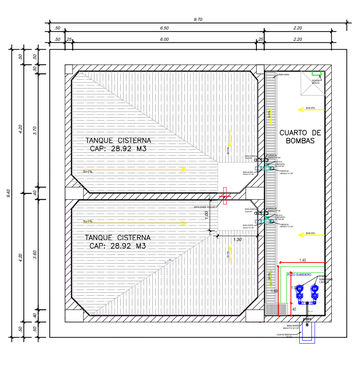

PLANTA CISTERNA – DRENAJE CUARTO BOMBAS

CORTE A–A (DESAGUE)

L E Y E N D A

- TUBERIA IMPULSION – SUCCION
- TUBERIA ALIMENTADOR
- VALVULA CHECK ENTRE UNIONES UNIVERSALES
- VALVULA COMPUERTA ENTRE UNIONES UNIVERSALES
- TUBERIA DE DESAGUE

CARACTERISTICAS DE EQUIPOS
DE BOMBEO
ELECTROBOMBAS SUMERGIBLES

DOS UNIDADES CADA UNA CON

GASTO (Q)	=	1.85 L.P.S. (3 M.S.)
POTENCIA (APROX.)	=	1.0HP – 220V 60c/s.
DIAMETRO IMPULSION	=	1 1/2"ø
ALTURA (H.D.T.)	=	7.00 mca.

CARACTERISTICAS DE EQUIPOS
DE BOMBEO
ELECTROBOMBAS CENTRIFUGAS PARA AGUA DE CONSUMO

Q	=	6.09 Lps.
Hdt	=	21.00 m
Pot. aprox.	=	3.0 HP.
N° de Unidades	=	2 (Uno Alternado)
N° de Polos	=	2
ø Impulsión	=	2 1/2"
VOLTAJE	=	220 Voltios
FRECUENCIA	=	60 Hertz

CARACTERISTICAS DE EQUIPOS
ELECTROBOMBAS PARA PRESURIZACION DE AGUA CALIENTE

Q	=	4.42 Lps.
Hdt	=	43.00 m
Pot. aprox.	=	5.0 HP.
N° de Unidades	=	2 (Uno Alternado)
N° de Polos	=	2
ø Impulsión	=	2"
VOLTAJE	=	220 Voltios
FRECUENCIA	=	60 Hertz

ESPECIFICACIONES TECNICAS DE TUBERIAS

1.– LAS TUBERIAS DE REBOSE, LIMPIA Y DESAGUE SERAN de Fo.Fo. PESADO, PINTADA CON DOBLE MANO DE PINTURA NEGRA (SERA Fo.Go En LOS TRAMOS QUE SE INDIQUE)

2.– LAS TUBERIAS DE AGUA (IMPULSION Y ALIMENTACION) SERAN DE Fo.Go.Ms.PESADO DEBIDAMENTE PINTADA CON DOBLE MANO DE PINTURA MARINA VERDE.

3.– LAS TUBERIAS DE SUCCION SERAN DE Fº Fº. PESADO (SEGUN PLANO).

4.– TODAS LAS TUBERIAS DE MONTAJE DE LAS BOMBAS SERAN DE Fo.Go. PESADO DEBIDAMENTE PINTADA CON DOBLE MANO DE PINTURA MARINA VERDE.

5.– LAS VALVULAS COMPUERTA, GLOBO Y FLOTADORAS SERAN CAPAZ DE SOPORTAR UNA PRESION DE TRABAJO DE 150 PSI.

ESPECIFICACIONES	OBSERVACION:
1.– SE CONSIDERA 1.5cm.DE ESPESOR DE TARRAJEO SOBRE LA ESTRUCTURA POR LO TANTO LAS COTAS INCLUYEN EL TARRAJEO.	ANTES DE LA RECEPCION DE LA OBRA ES NECESARIO QUE SE EFECTUE LA PRUEBA HIDRAULICA DE ESTANQUIDAD Y DESINFECCION DE LA CISTERNA Y TANQUE ELEVADO.
2.– TAPA METALICA DE LA CISTERNA Y TANQUE ELEVADO. – FABRICADAS CON PLANCHA METALICA LAF e=1/16". – CON 2 MANOS DE PINTURA ANTICORROSIVO ROJO/PRIMER. – Con abrazo con perno y nuez. – CON 2 MANOS DE PINTURA ESMALTE (color bajo a gris oscuro. – BISAGRAS FABRICADAS EN TALLER. – 1 CANDADO PESADO 80mm. Y OREJAS PORTACANDADOS.	

Escuela Provincial Educación Técnica N°4 O.E.A	Materia: Proyecto IV	6 Año A Maestro Mayor de Obra	**Proyecto: Edificios sociales e intervención urbana, Andres Gaspar Giai**
Profesor Asesor: Gustavo Yanssen	Equipo de Proyecto:	Amarilla Carlos, Antunez Gonzalo, Barrios Alan y Beling Alexander	Titulo lamina: Instalación Sanitaria y Detalles de tanque
Fecha de inicio: 8/10/24	Fecha de finalización: 13/11/24	Fecha de presentación al publico: 14/11/24	Fecha de relevamiento: 1/10/24	Numero lamina: 4

PLANTA DE TECHO SANITARIA

ESC. 1:100

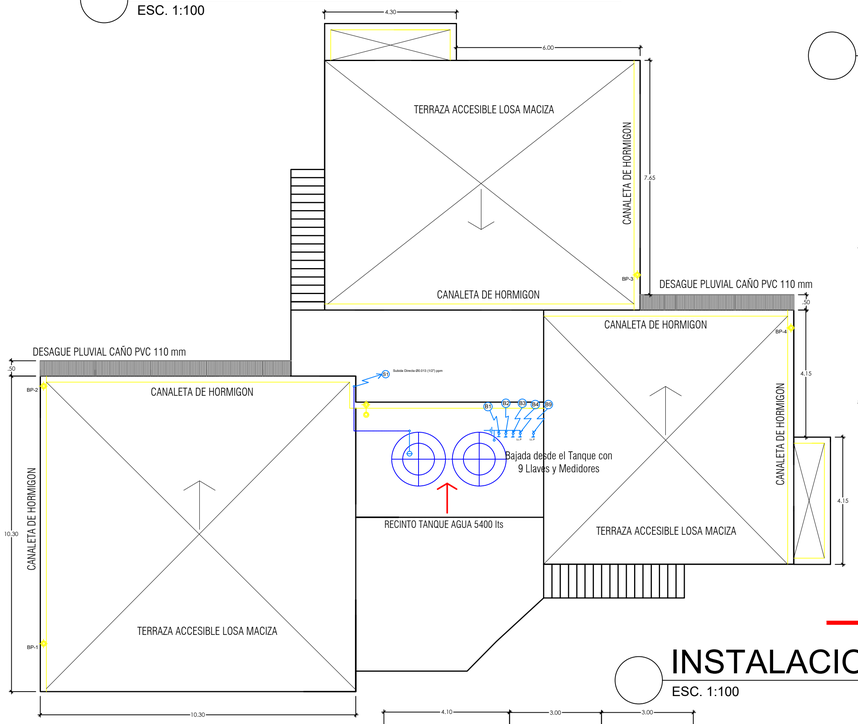

FUNDACIONES 3

ESC. 1:100

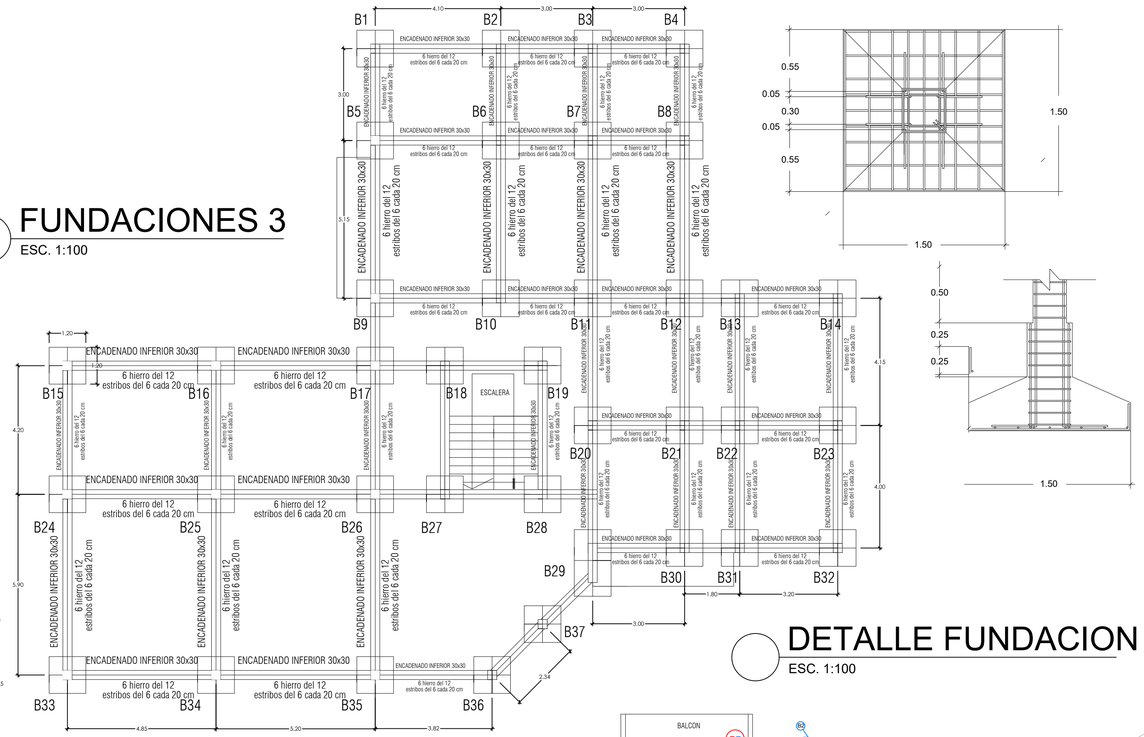

DETALLE FUNDACION

ESC. 1:100

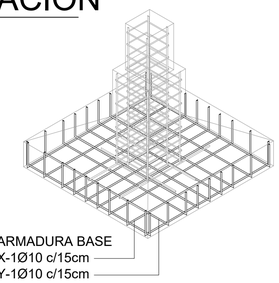

INSTALACIONES SANITARIAS PLANTA BAJA

ESC. 1:100

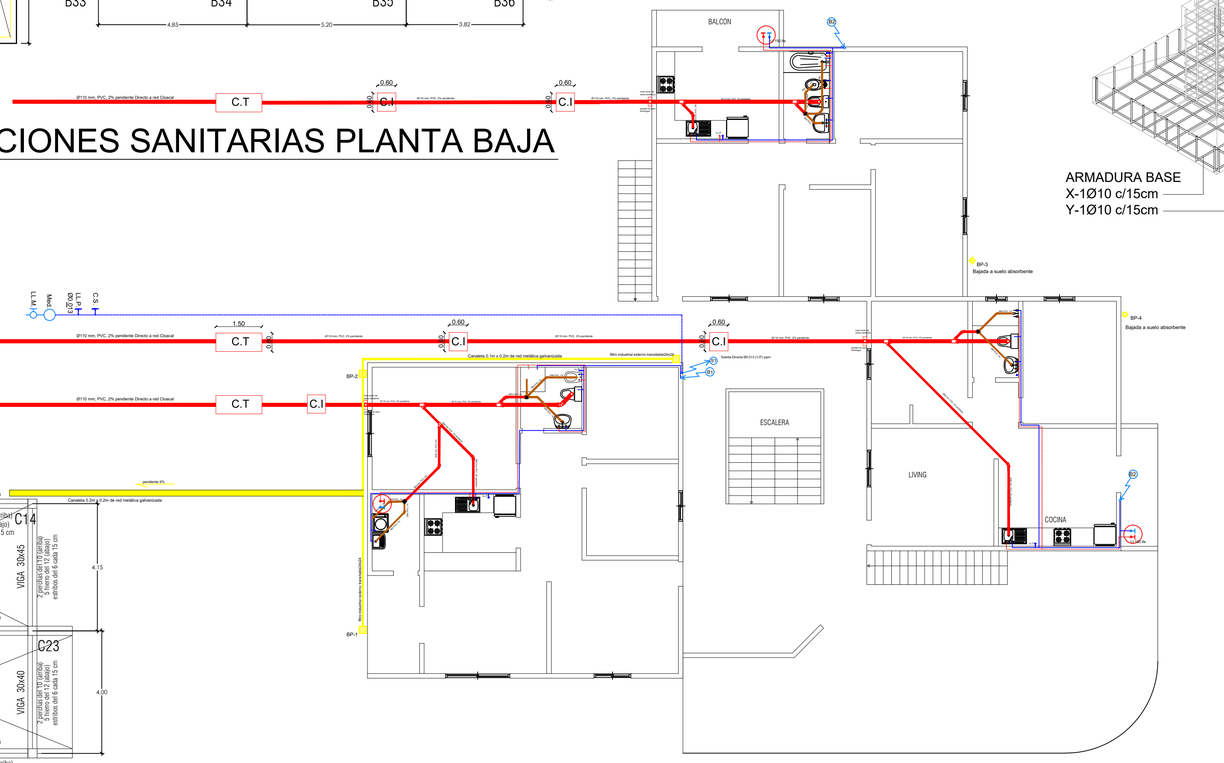

VIGAS PLNATA BAJA

ESC. 1:100

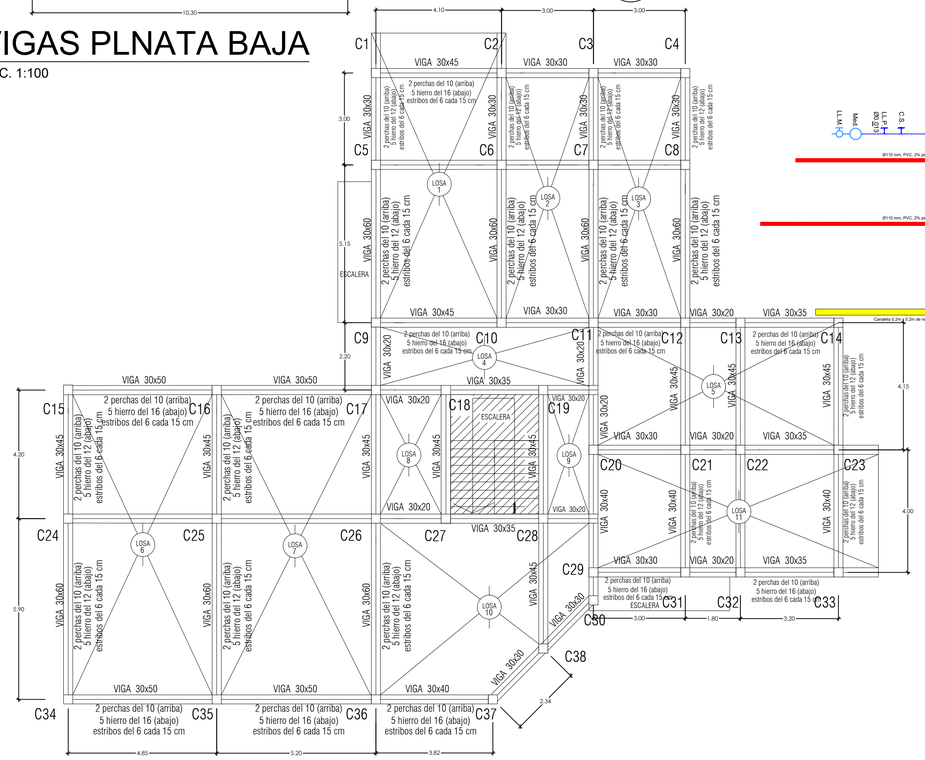

Escuela Provincial Educación Técnica N°4 O.E.A	Materia: Proyecto IV	6 Año A Maestro Mayor de Obra	**Proyecto: Edificios sociales e intervención urbana, Andres Gaspar Giai**
Profesor Asesor: Gustavo Yanssen	Equipo de Proyecto:	Amarilla Carlos, Antunez Gonzalo, Barrios Alan y Beling Alexander	Titulo lamina: Replanteo e Instalaciones Sanitarias
Fecha de inicio: 8/10/24	Fecha de finalización: 13/11/24	Fecha de presentación al publico: 14/11/24	Fecha de relevamiento: 1/10/24	Numero lamina: 5

VIGAS PLNATA PRIMER PISO

ESC. 1:100

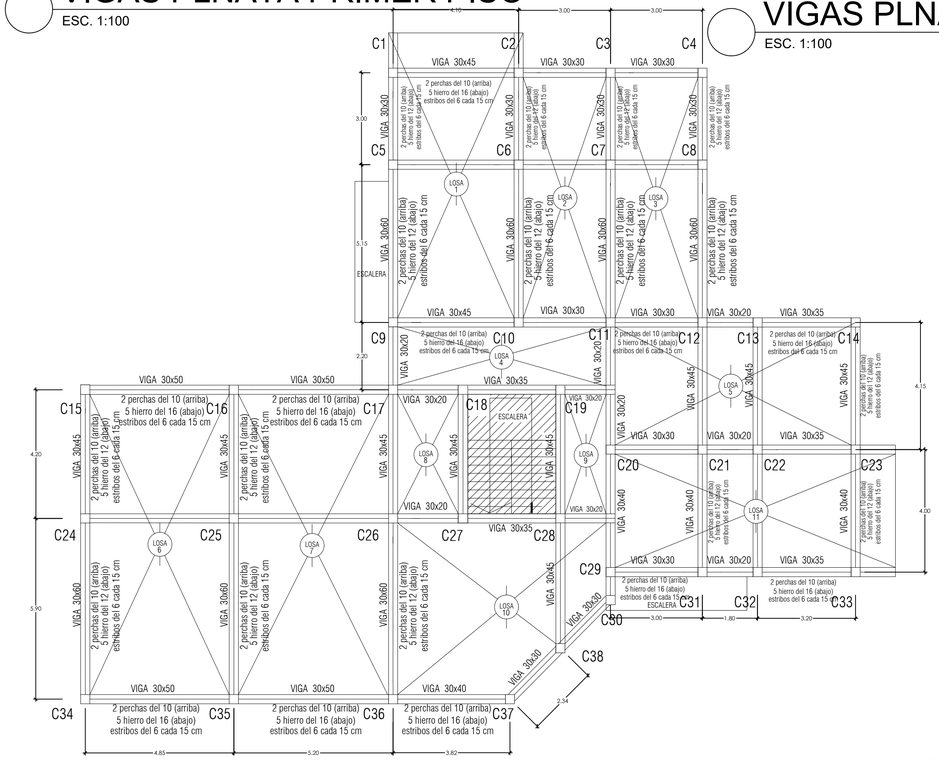

VIGAS PLNATA SEGUNDO PISO

ESC. 1:100

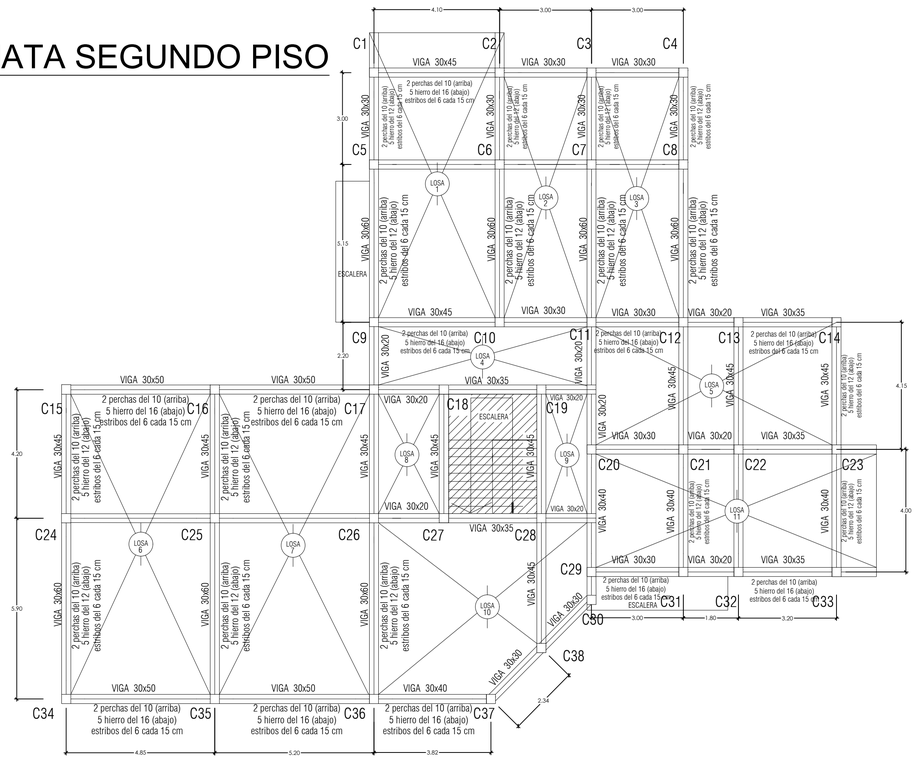

INSTALACIONES ELECTRICAS 3

ESC. 1:100

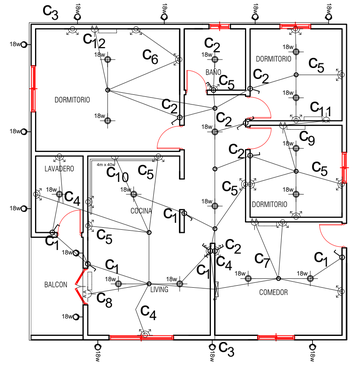

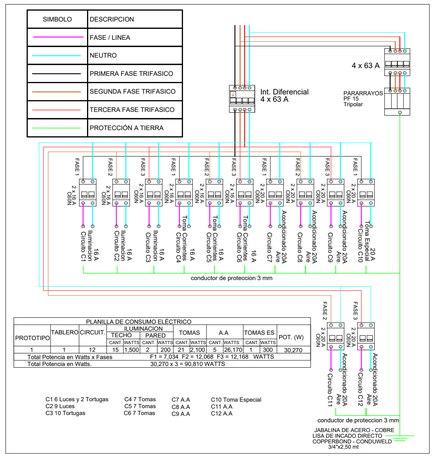

Simbologia	Descripción	Altura m
18w	SALIDA DE ILUMINACIÓN EN TECHO	TECHO
18w	SALIDA DE ILUMINACIÓN EN PARED TIPO TORTUGA	TECHO
	TOMA CORRIENTES BIPOLAR DOBLE/CON LÍNEA A TIERRA, A PRUEBA DE HUMEDAD TOMA ATERRIZADA ISA 220V CON TAPA FRONTAL, GRADO DE PROTECCIÓN IP55	0.40
	TOMA CORRIENTES BIPOLAR CON LÍNEA A TIERRA, TOMA ATERRIZADA 20A APRUEBA DE HUMEDAD, TOMA ATERRIZADA 20A CON TAPA FRONTAL GRADO DE PROTECCIÓN IP55 SIMILAR	1
	INTERRUPTOR DE LUCES UNIPOLAR	1.20
	CONMUTADOR DE LUCES UNIPOLAR	1.20
	CAJA DE DISTRIBUCIÓN DIFERENCIAL PRINCIPAL	1.20
	CAJA OCTOGONAL CONTENEDOR ELÉCTRICO	TECHO
	AIRE ACONDICIONADO DE 4500 REFRIGERIOS	2.10
AA	TOMA CORRIENTES BIPOLAR CON LÍNEA A TIERRA, TOMA ATERRIZADA 20A A PRUEBA DE HUMEDAD, TOMA ATERRIZADA 20A CON TAPA FRONTAL GRADO DE PROTECCIÓN IP55 SIMILAR	2.10
m x 10w	Kit Manguera Luz Neon Fuente + Ficha Interior	2.10

INSTALACIONES ELECTRICAS 4

ESC. 1:100

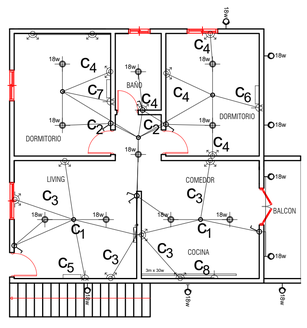

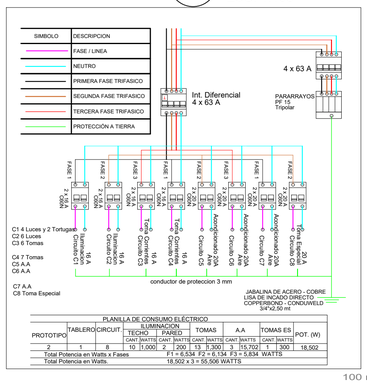

Transformador de 1600kw de baja tensión de 220v - 380v

Principal 700kw
Secundarios 810kw
Zona de servicio 9kw

perforación 100m 4hp = 4kw x 2 = 8kw
Bombas superior 1.5hp = 1.5kw x 2 = 3kw

1519kw +15% (futuras expansiones) = 1746.85kw x 0.92 (coeficiente) = 1607.102kw x 0.95 (uso no simultáneo) = 1526.7469kw

INSTALACIONES SANITARIAS PLANTA PRIMER PISO

ESC. 1:100

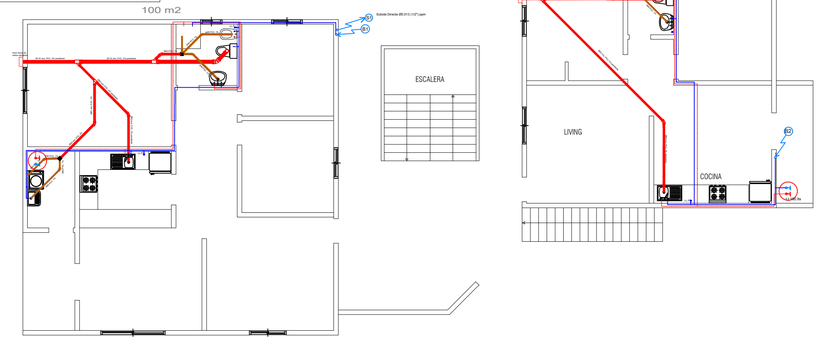
100 m2
ESCALERA
LIVING
COCINA
BALCON
Salida Directa Ø0.15 (10.2%)
Ø0.15 (10.2%) Ascendente
Ø0.15 (10.2%) Descendente
Ø0.10 (10.2%) Ascendente
Ø0.10 (10.2%) Descendente
Ø0.10 (10.2%) Horizontal
Ø0.10 (10.2%) Vertical
Ø0.10 (10.2%) Vertical Ventilación
Ø0.10 (10.2%) Vertical Ventilación Descendente
Ø0.10 (10.2%) Vertical Ventilación Ascendente
Ø0.10 (10.2%) Vertical Ventilación Horizontal
Ø0.10 (10.2%) Vertical Ventilación Horizontal Descendente
Ø0.10 (10.2%) Vertical Ventilación Horizontal Ascendente
Ø0.10 (10.2%) Vertical Ventilación Horizontal Descendente Ascendente
Ø0.10 (10.2%) Vertical Ventilación Horizontal Descendente Ascendente Horizontal
Ø0.10 (10.2%) Vertical Ventilación Horizontal Descendente Ascendente Horizontal Vertical
Ø0.10 (10.2%) Vertical Ventilación Horizontal Descendente Ascendente Horizontal Vertical Ventilación
CORTE LONGITUDINAL EDIFICIO PRINCIPAL

ESC. 1:100

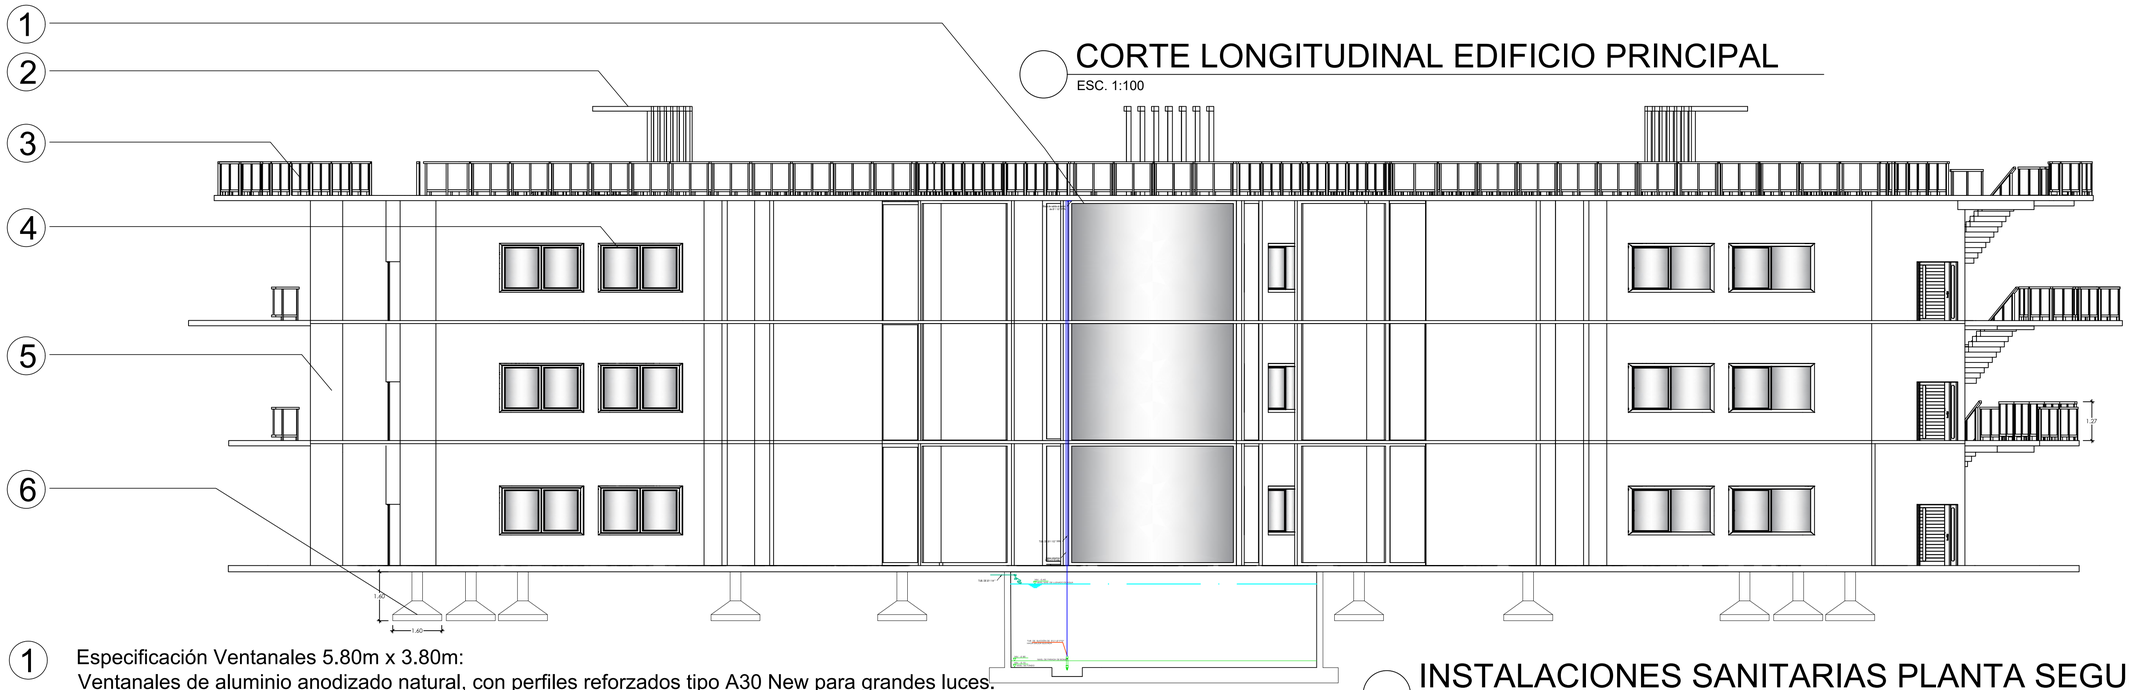

1 Especificación Ventanales 5.80m x 3.80m:
Ventanales de aluminio anodizado natural, con perfiles reforzados tipo A30 New para grandes luces.
Vidrio doble vidriado hermético
(DVH) 4+12+4 mm, compuesto por vidrio exterior laminado (4+4 mm) y vidrio interior templado, garantizando seguridad y aislamiento térmico/acústico. Herrajes de acero inoxidable con cierres multipunto. Sellado perimetral con juntas de EPDM y siliconaestructural resistente a la intemperie.

2 Pérgola Terraza Verde:
Pérgola de madera dura tratada para intemperie (lapacho) con acabado protector tipo barniz marino.Estructura de 2.85 m de alto, con columnas laminadas de 15x15 cm, ancladas a la losa mediante zapatas metálicas galvanizadas y fijación química al hormigón. Vigas principales de 10x20 cm y vigas secundarias de 5x15 cm, dispuestas cada 50 cm. Cubierta con enrejado de listones de 5x5 cm, preparada para vegetación trepadora y sistema de riego. Uniones con tornillos de acero inoxidable y escuadras metálicas ocultas, selladas con silicona neutra. Estructura diseñada para soportar carga vegetal y alta humedad en clima subtropical.

3 Baranda de aluminio anodizado, con soportes cada 1.20 m y vidrio laminado 5+5 mm, fijado con herrajes tipo U y silicona estructural. Altura de 1.30m desde el piso, anclada a la losa con tacos químicos y pernos expansivos de acero inoxidable. Pasamanos continuo de aluminio, con uniones ocultas en esquinas y encuentros. Diseñada para resistir cargas de viento y uso en exteriores con alta humedad.

4 Ventanas de aluminio anodizado, con perfiles tipo A30 New. Vidrio doble vidriado hermético (DVH) 4+12+4 mm, compuesto por vidrio exterior laminado (4+4 mm) y vidrio interior templado, para seguridad y aislamiento térmico/acústico. Herrajes de acero inoxidable con cierres multipunto. Sellado perimetral con juntas de EPDM y silicona estructural resistente a la intemperie. Anclaje mediante tacos químicos y fijación oculta al marco estructural.

5 Revestimiento de laja natural en placas irregulares, instalado con adhesivo cementicio flexible apto para exteriores. Anclaje adicional mediante fijaciones mecánicas ocultas en zonas de mayor exposición. Sellado de juntas con mortero impermeable para evitar filtraciones. Tratamiento final con impermeabilizante transparente para protección contra humedad y hongos.

6 Fundación mediante zapatas aisladas de 1.60 m x 1.60 m, armadas con acero de refuerzo longitudinal y estribos perimetrales. Las zapatas se vinculan a las columnas mediante pedestales de hormigón armado. Hormigón de resistencia H25, con asentamiento adecuado para garantizar la estabilidad de la estructura que soporta 3 pisos más una terraza. La base se apoya sobre terreno compactado y nivelado, con capa de limpieza de hormigón pobre (H8). Impermeabilización en los bordes para evitar la absorción de humedad del subsuelo.

INSTALACIONES SANITARIAS PLANTA SEGUNDO PISO

ESC. 1:100

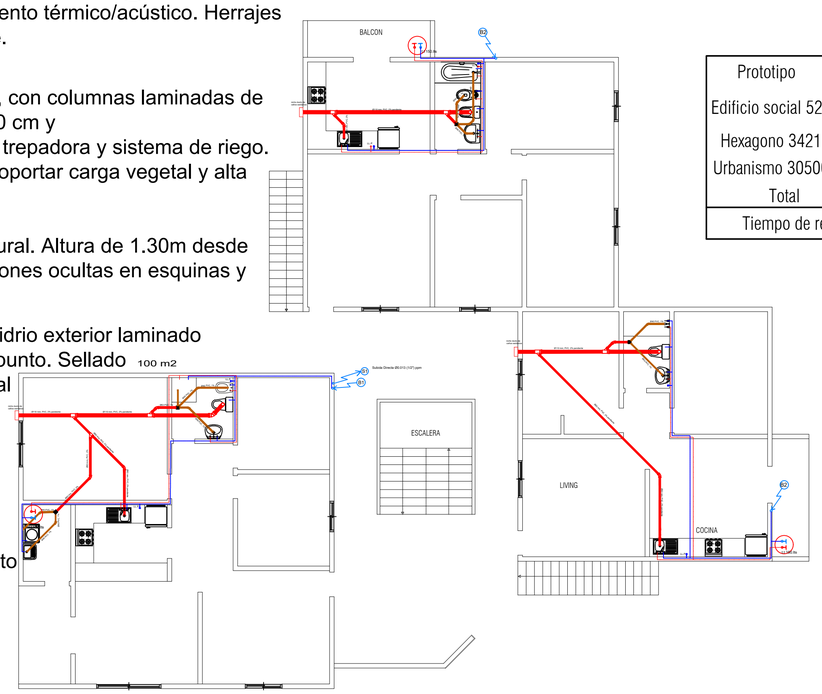

Prototipo	Presupuesto
Edificio social 525 m2	638.925.000ARS
Hexagono 3421 m2	4.163.357.000ARS
Urbanismo 30500 m2	27.450.000.000ARS
Total	32.252.282.000ARS
Tiempo de realización 3 a 6 años	

Escuela Provincial Educación Técnica N°4 O.E.A		Materia: Proyecto IV	6 Año A Maestro Mayor de Obra	**Proyecto: Edificios sociales e intervención urbana, Andres Gaspar Giai**
Profesor Asesor: Gustavo Yanssen		Equipo de Proyecto:	Amarilla Carlos, Antunez Gonzalo, Barrios Alan y Beling Alexander	Titulo lamina: Corte longitudinal e instalación Sanitaria
Fecha de inicio: 8/10/24	Fecha de finalización: 13/11/24	Fecha de presentación al publico: 14/11/24	Fecha de relevamiento: 1/10/24	Numero lamina: 7

PLANTA BAJA EDIFICIO PRINCIPAL

ESC. 1:120

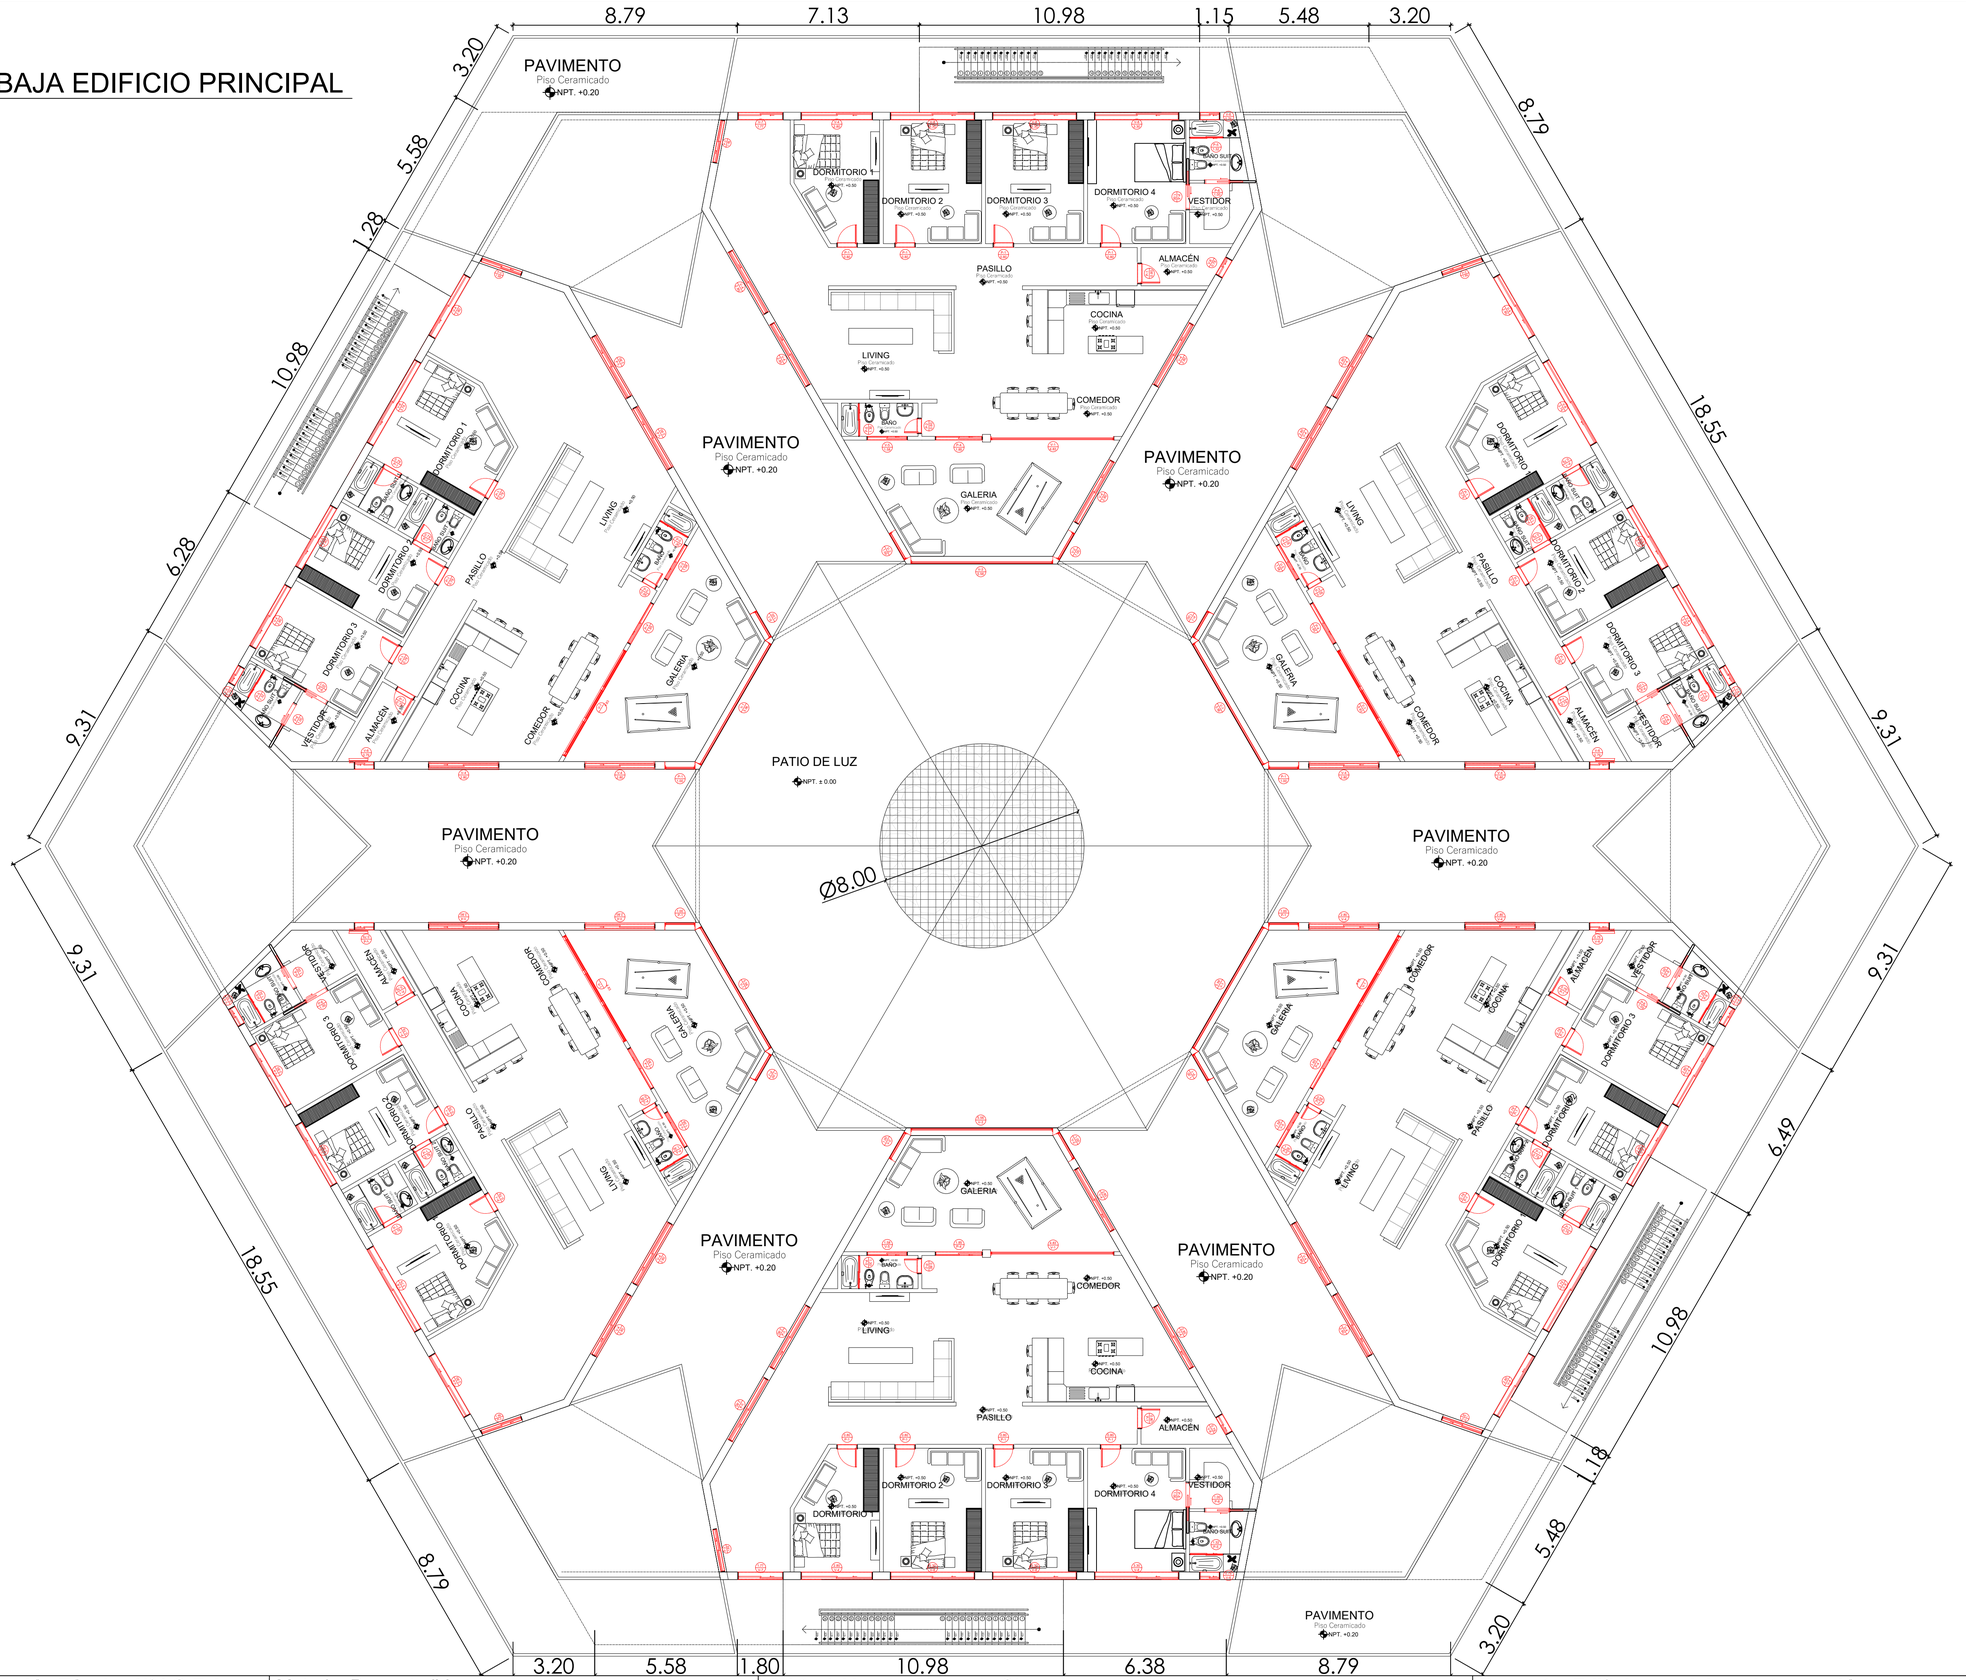

Escuela Provincial Educación Técnica N°4 O.E.A		Materia: Proyecto IV	6 Año A Maestro Mayor de Obra	**Proyecto: Edificios sociales e intervención urbana, Andres Gaspar Giai**
Profesor Asesor: Gustavo Yanssen		Equipo de Proyecto:	Amarilla Carlos, Antunez Gonzalo, Barrios Alan y Beling Alexander	Titulo lamina: Planta baja de edificio principal
Fecha de inicio: 8/10/24	Fecha de finalización: 13/11/24	Fecha de presentación al publico: 14/11/24	Fecha de relevamiento: 1/10/24	Numero lamina: 8

PLANTA 1ER PISO EDIFICIO PRINCIPAL

ESC. 1:120

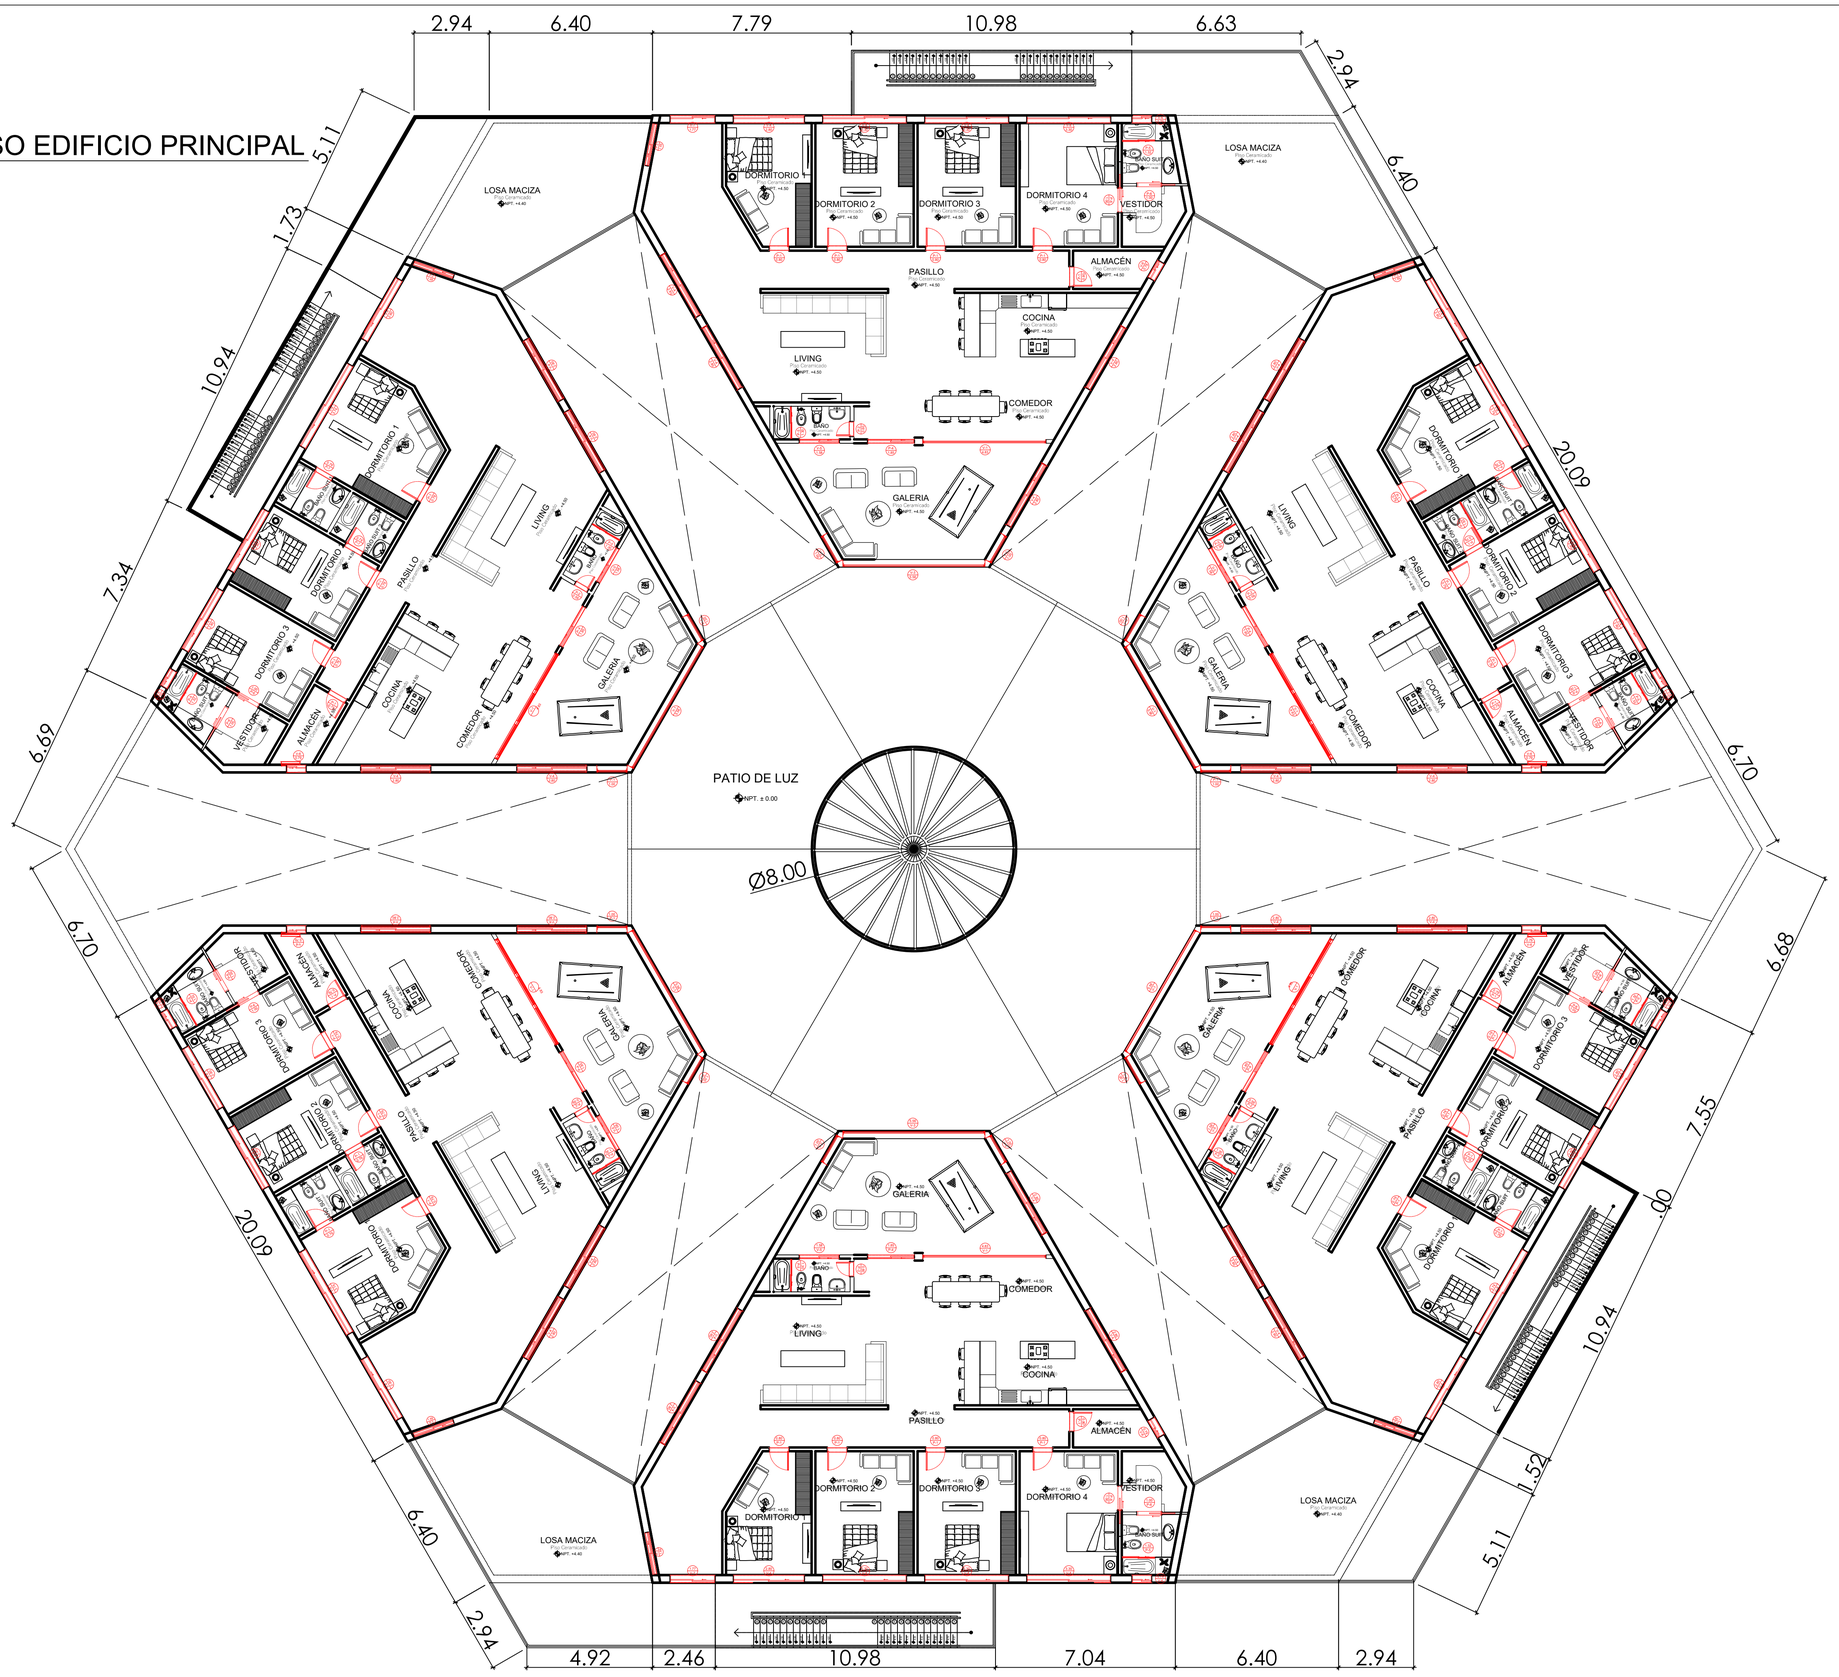

Escuela Provincial Educación Técnica N°4 O.E.A	Materia: Proyecto IV	6 Año A Maestro Mayor de Obra	**Proyecto: Edificios sociales e intervención urbana, Andres Gaspar Giai**
Profesor Asesor: Gustavo Yanssen	Equipo de Proyecto:	Amarilla Carlos, Antunez Gonzalo, Barrios Alan y Beling Alexander	Titulo lamina: Planta de 1er piso de edificio principal
Fecha de inicio: 8/10/24 — Fecha de finalización: 13/11/24	Fecha de presentación al publico: 14/11/24	Fecha de relevamiento: 1/10/24	Numero lamina: 9

PLANTA 2DO PISO EDIFICIO PRINCIPAL

ESC. 1:120

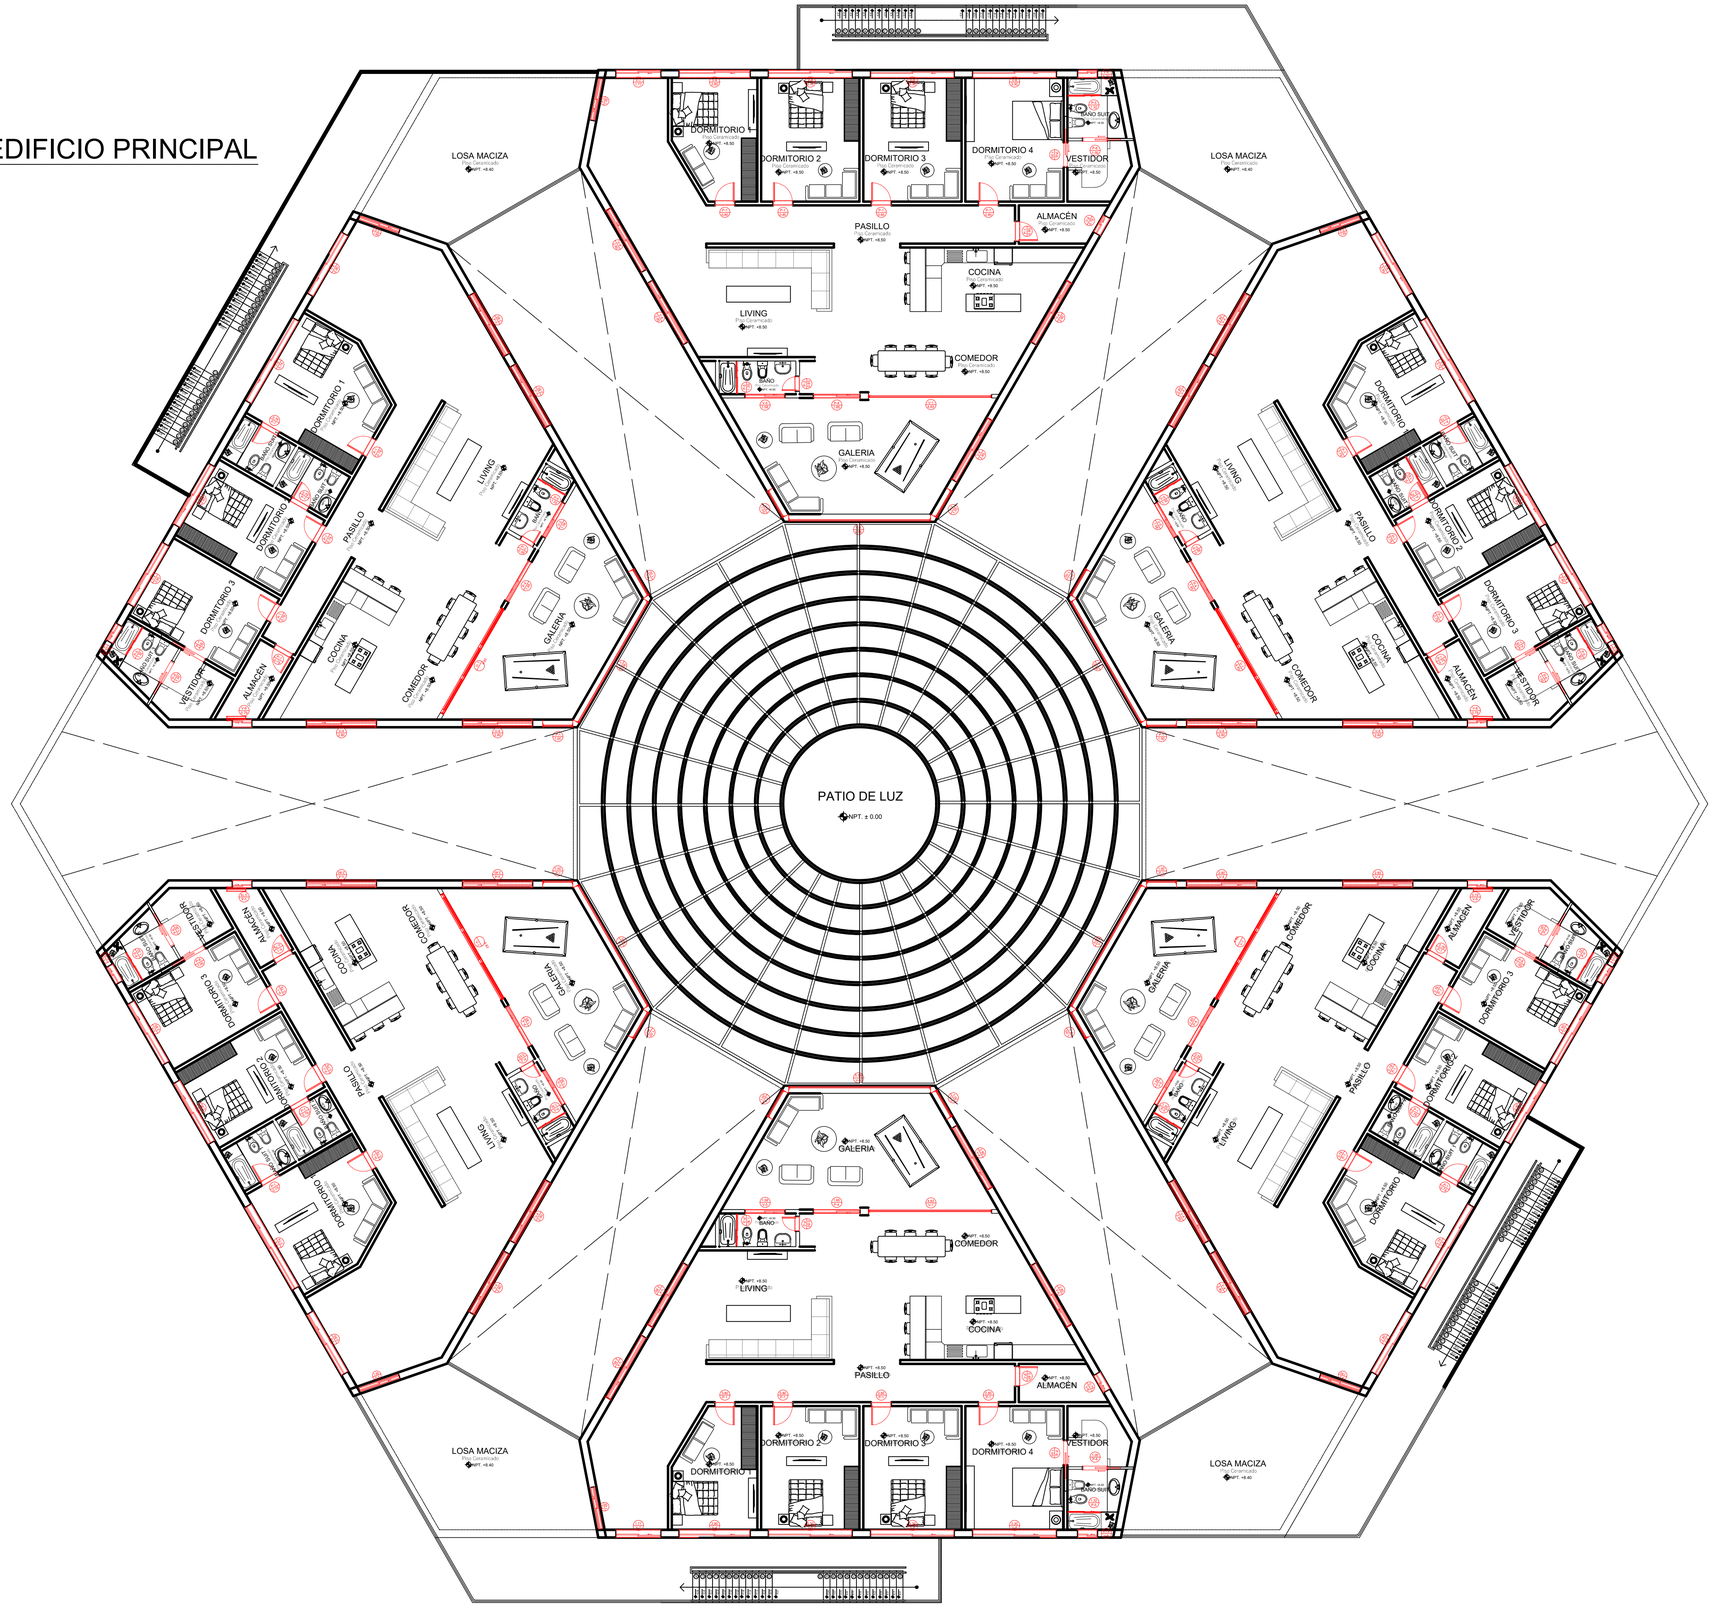

Escuela Provincial Educación Técnica N°4 O.E.A		Materia: Proyecto IV	6 Año A Maestro Mayor de Obra	**Proyecto: Edificios sociales e intervención urbana, Andres Gaspar Giai**
Profesor Asesor: Gustavo Yanssen		Equipo de Proyecto:	Amarilla Carlos, Antunez Gonzalo, Barrios Alan y Beling Alexander	Titulo lamina: Planta 2do piso de edificio principal
Fecha de inicio: 8/10/24	Fecha de finalización: 13/11/24	Fecha de presentación al publico: 14/11/24	Fecha de relevamiento: 1/10/24	Numero lamina: 10

PLANTA TERRAZA

ESC. 1:120

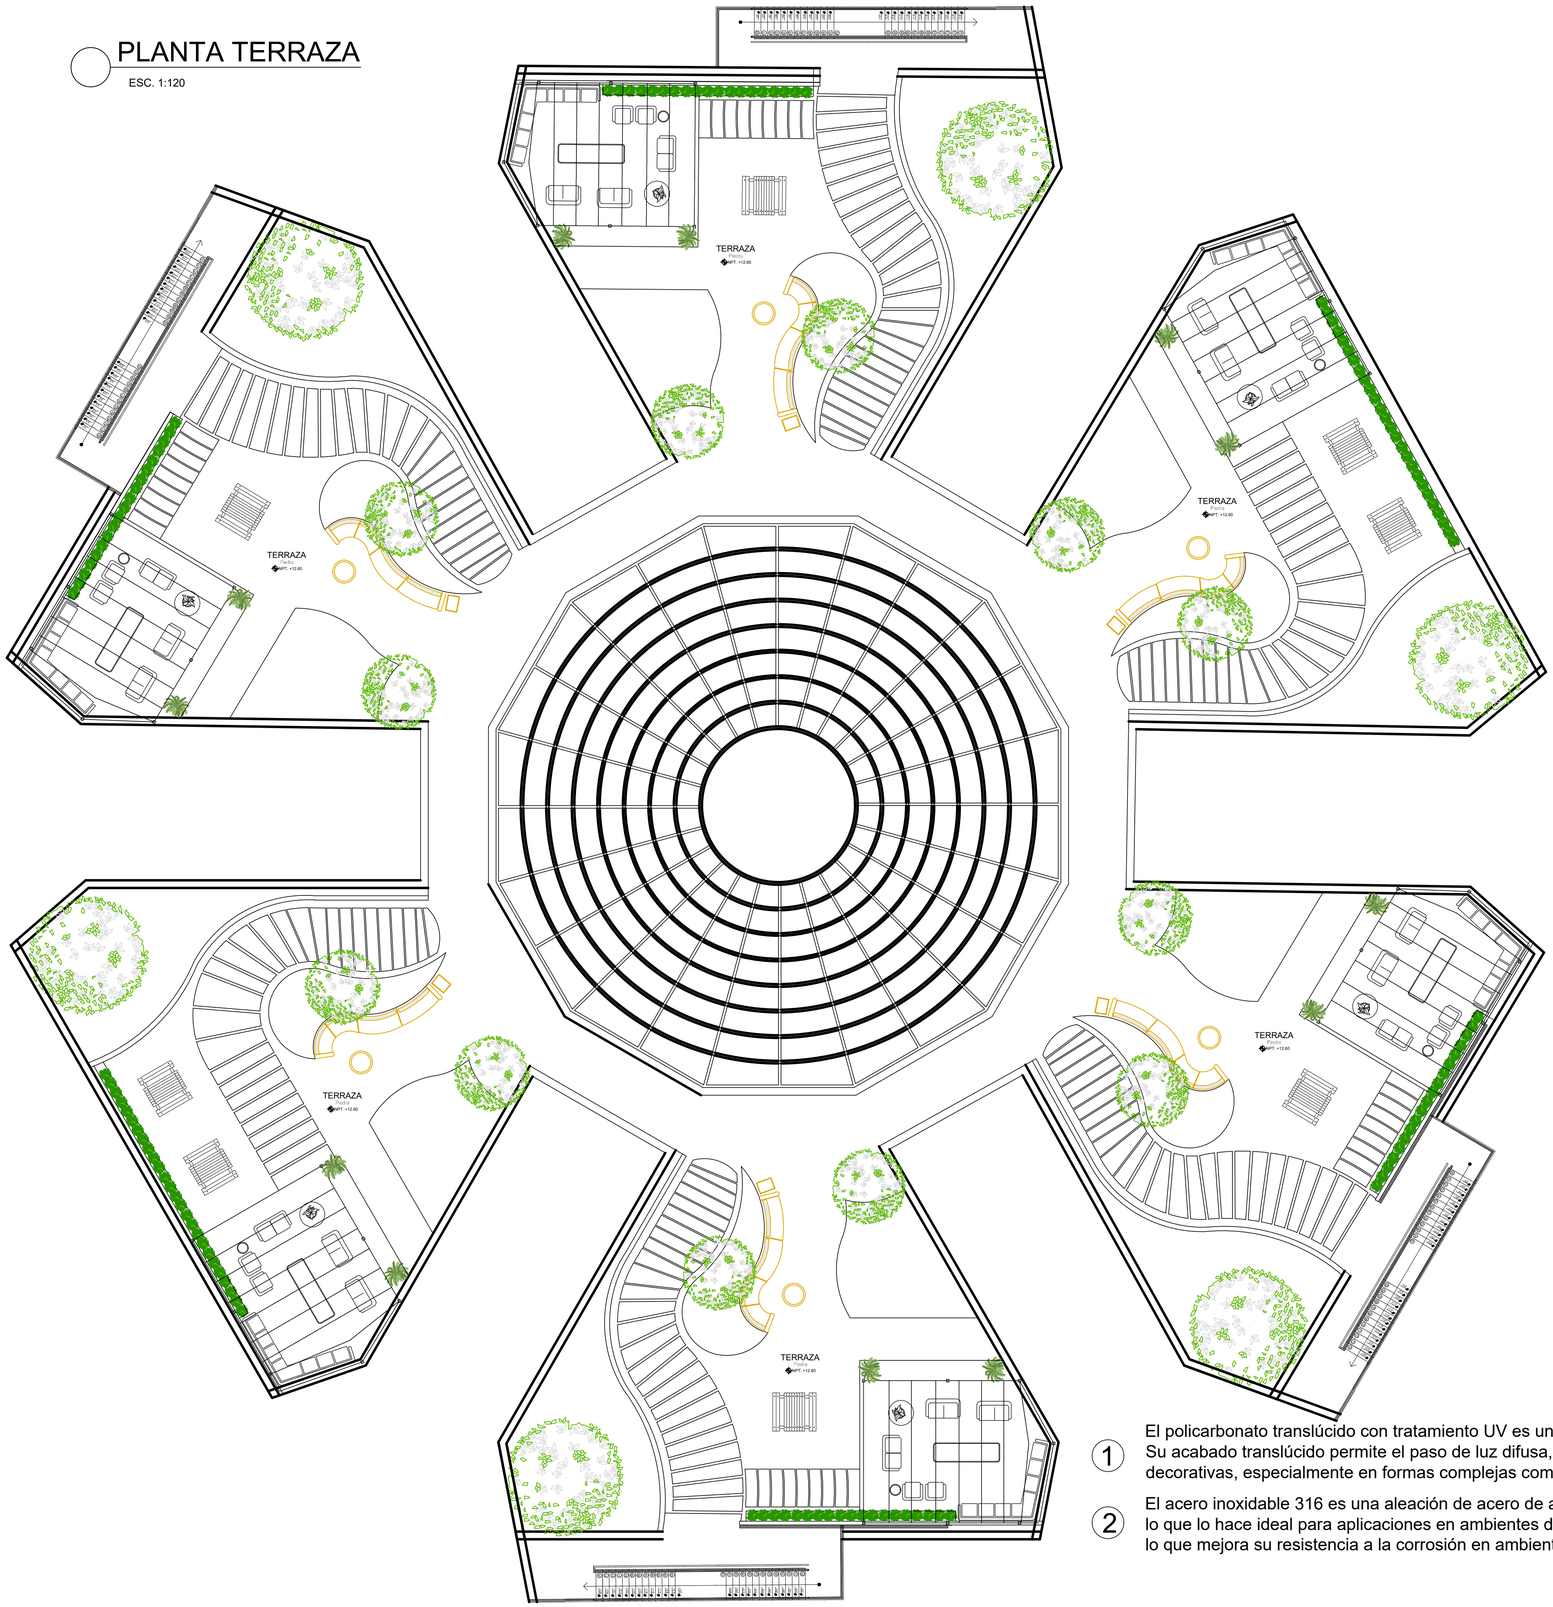

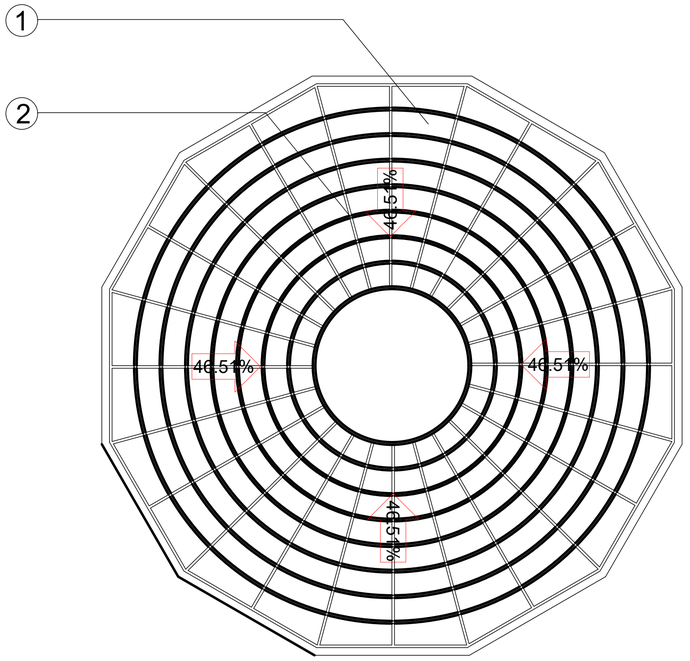

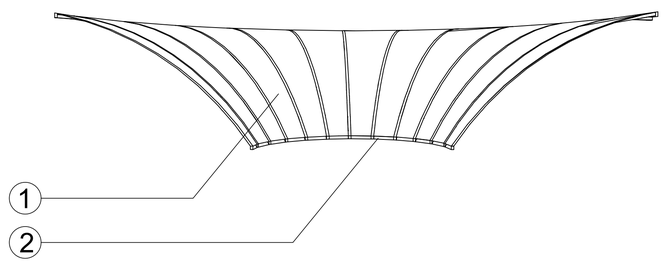

1. El policarbonato translúcido con tratamiento UV es un material termoplástico de alta resistencia al impacto y a las condiciones ambientales. Su acabado translúcido permite el paso de luz difusa, proporcionando una estética moderna y funcional. Es ideal para aplicaciones estructurales y decorativas, especialmente en formas complejas como hipérbolas.

2. El acero inoxidable 316 es una aleación de acero de alta calidad, conocida por su resistencia a la corrosión y a condiciones extremas, lo que lo hace ideal para aplicaciones en ambientes difíciles. Es una variante mejorada del acero inoxidable 304, gracias a la adición de molibdeno, lo que mejora su resistencia a la corrosión en ambientes con cloro y productos químicos agresivos.

Escuela Provincial Educación Técnica N°4 O.E.A		Materia: Proyecto IV	6 Año A Maestro Mayor de Obra	**Proyecto: Edificios sociales e intervención urbana, Andres Gaspar Giai**
Profesor Asesor: Gustavo Yanssen		Equipo de Proyecto:	Amarilla Carlos, Antunez Gonzalo, Barrios Alan y Beling Alexander	Titulo lamina: Planta de terraza de edificio principal
Fecha de inicio: 8/10/24	Fecha de finalización: 13/11/24	Fecha de presentación al publico: 14/11/24	Fecha de relevamiento: 1/10/24	Numero lamina: 11

CLOACALES

ESC. 1:300

Poso perforador.

PAVIMENTO

Perforacion

LAGO ARTIFICIAL

cámaras de inspección con conexiones múltiples

Escuela Provincial Educación Técnica N°4 O.E.A	Materia: Proyecto IV	6 Año A Maestro Mayor de Obra	**Proyecto: Edificios sociales e intervención urbana, Andres Gaspar Giai**
Profesor Asesor: Gustavo Yanssen	Equipo de Proyecto:	Amarilla Carlos, Antunez Gonzalo, Barrios Alan y Beling Alexander	Titulo lamina: Instalaciones cloacales en Urbanismo y Terreno
Fecha de inicio: 8/10/24 — Fecha de finalización: 13/11/24	Fecha de presentación al publico: 14/11/24	Fecha de relevamiento: 1/10/24	Numero lamina: 12