
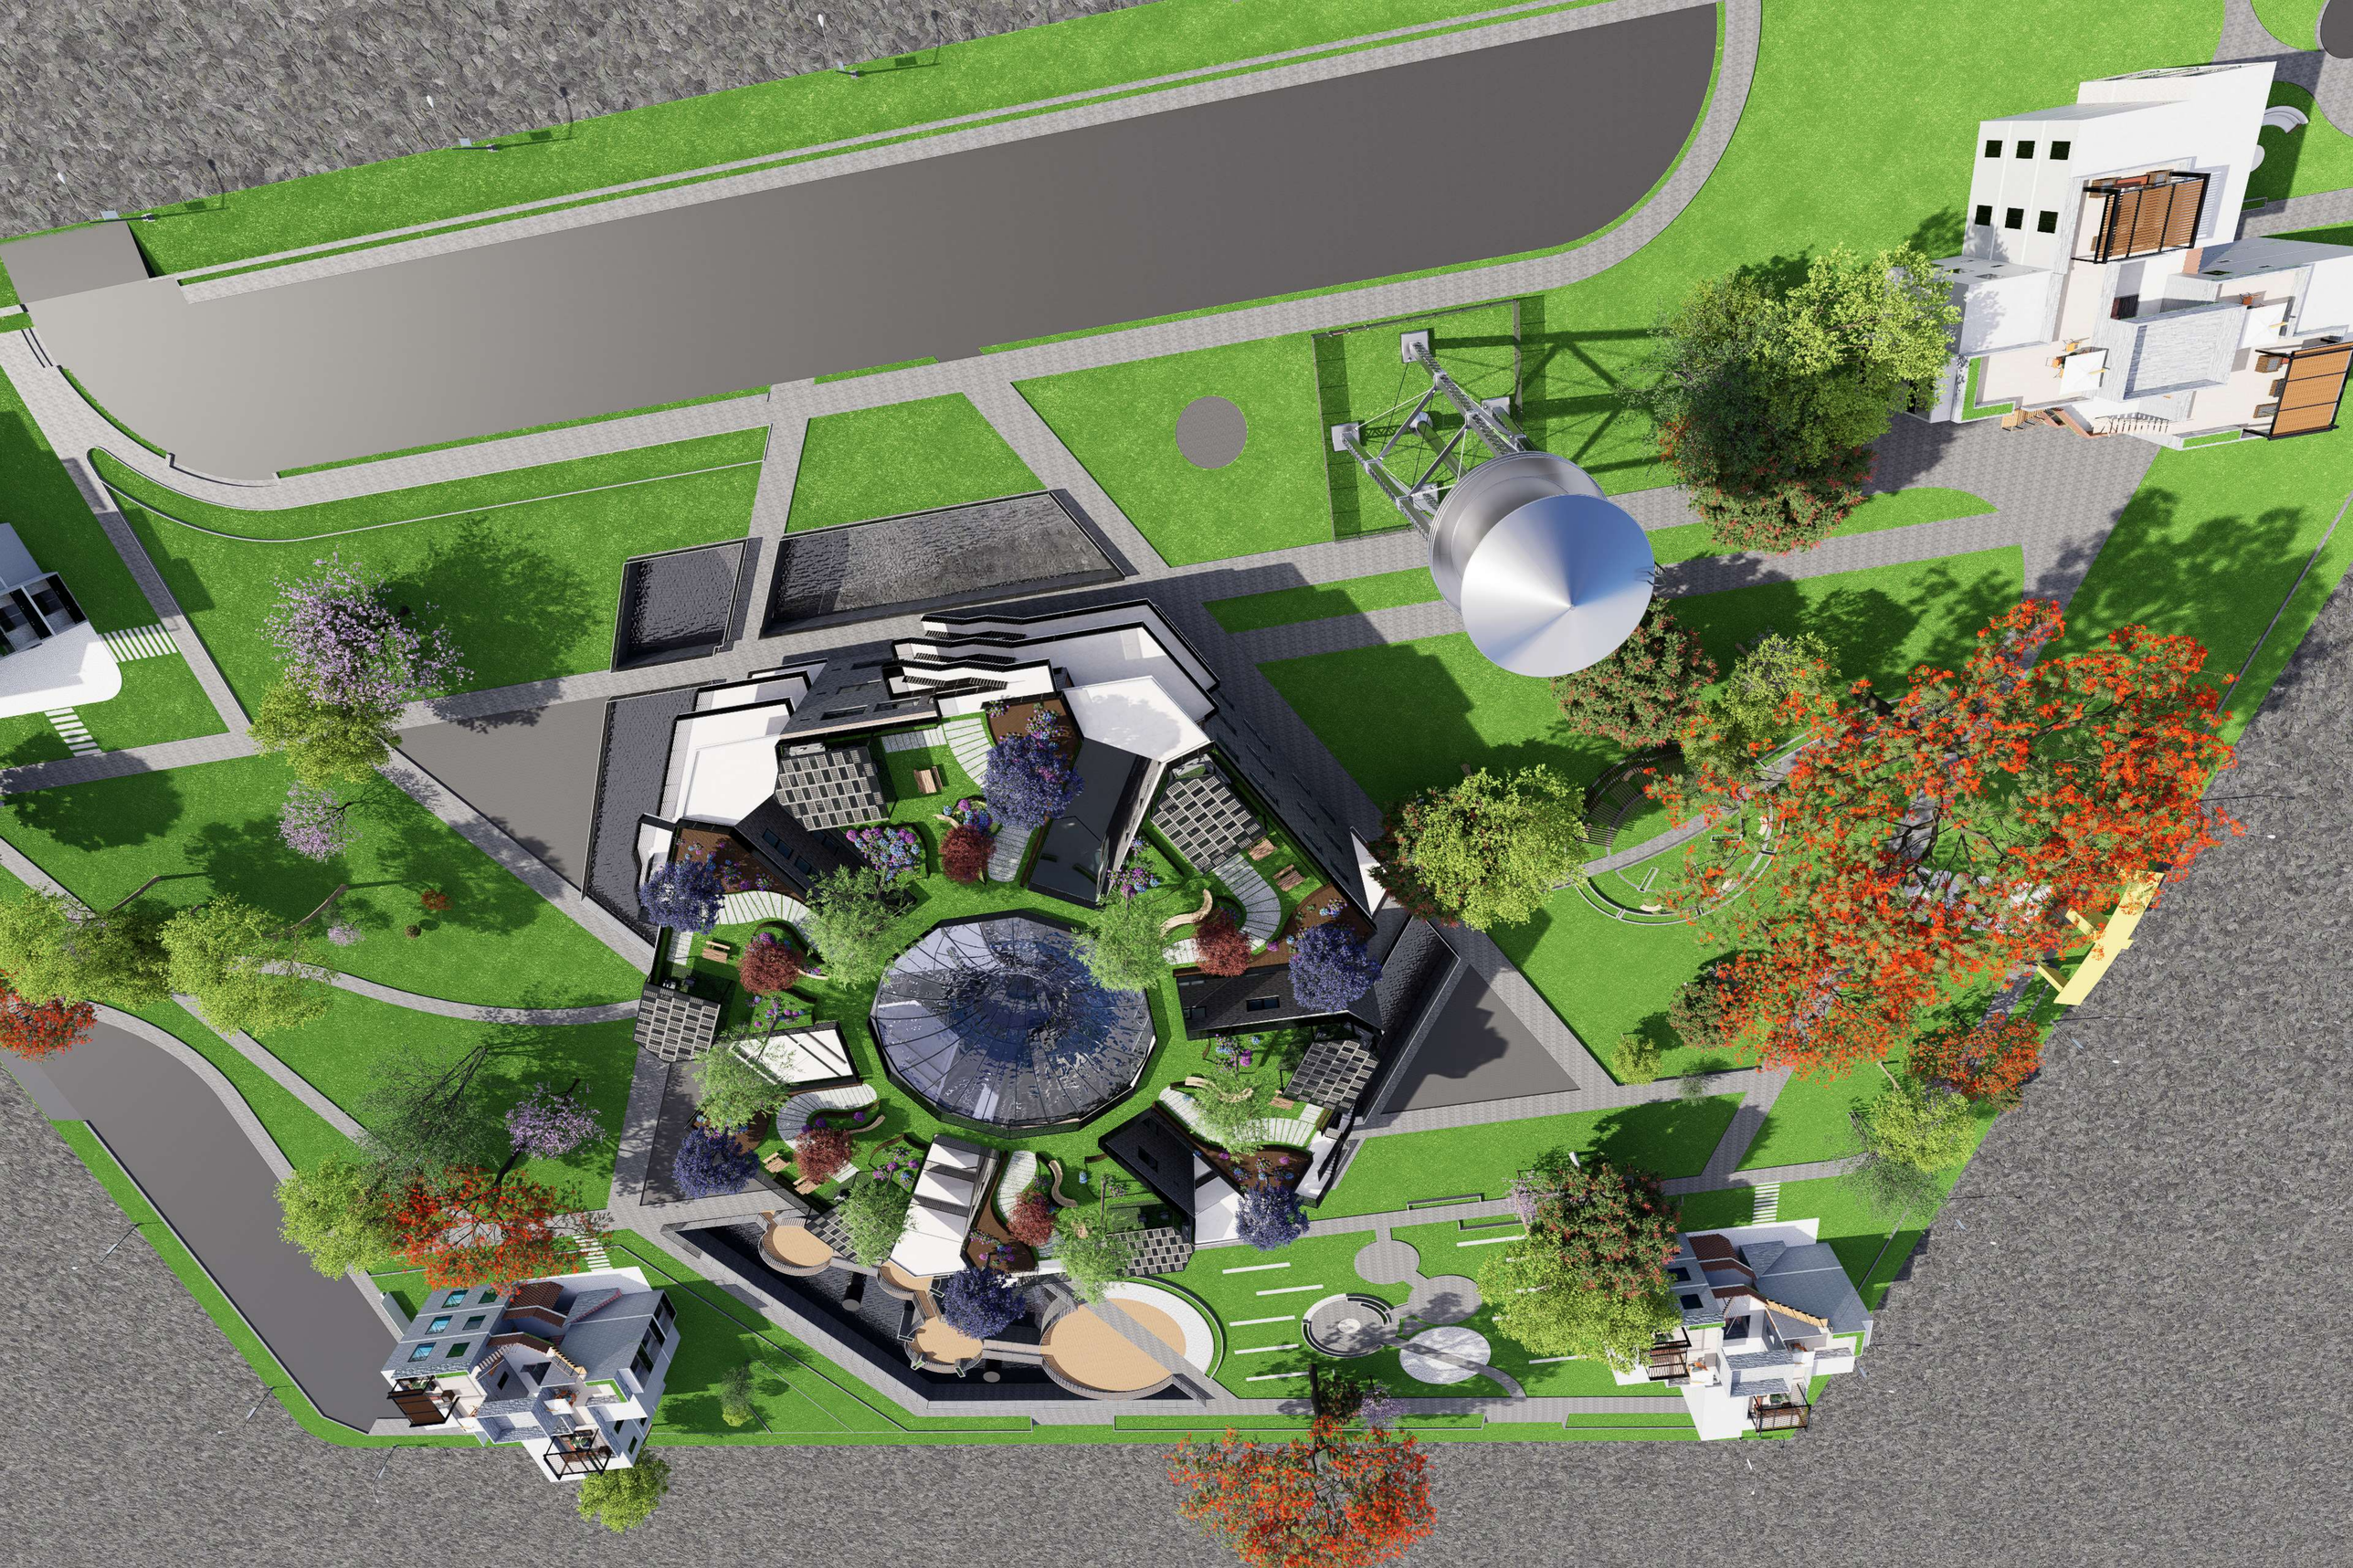


CORTE LONGITUDINAL EDIFICIO PRINCIPAL

ESC. 1:100

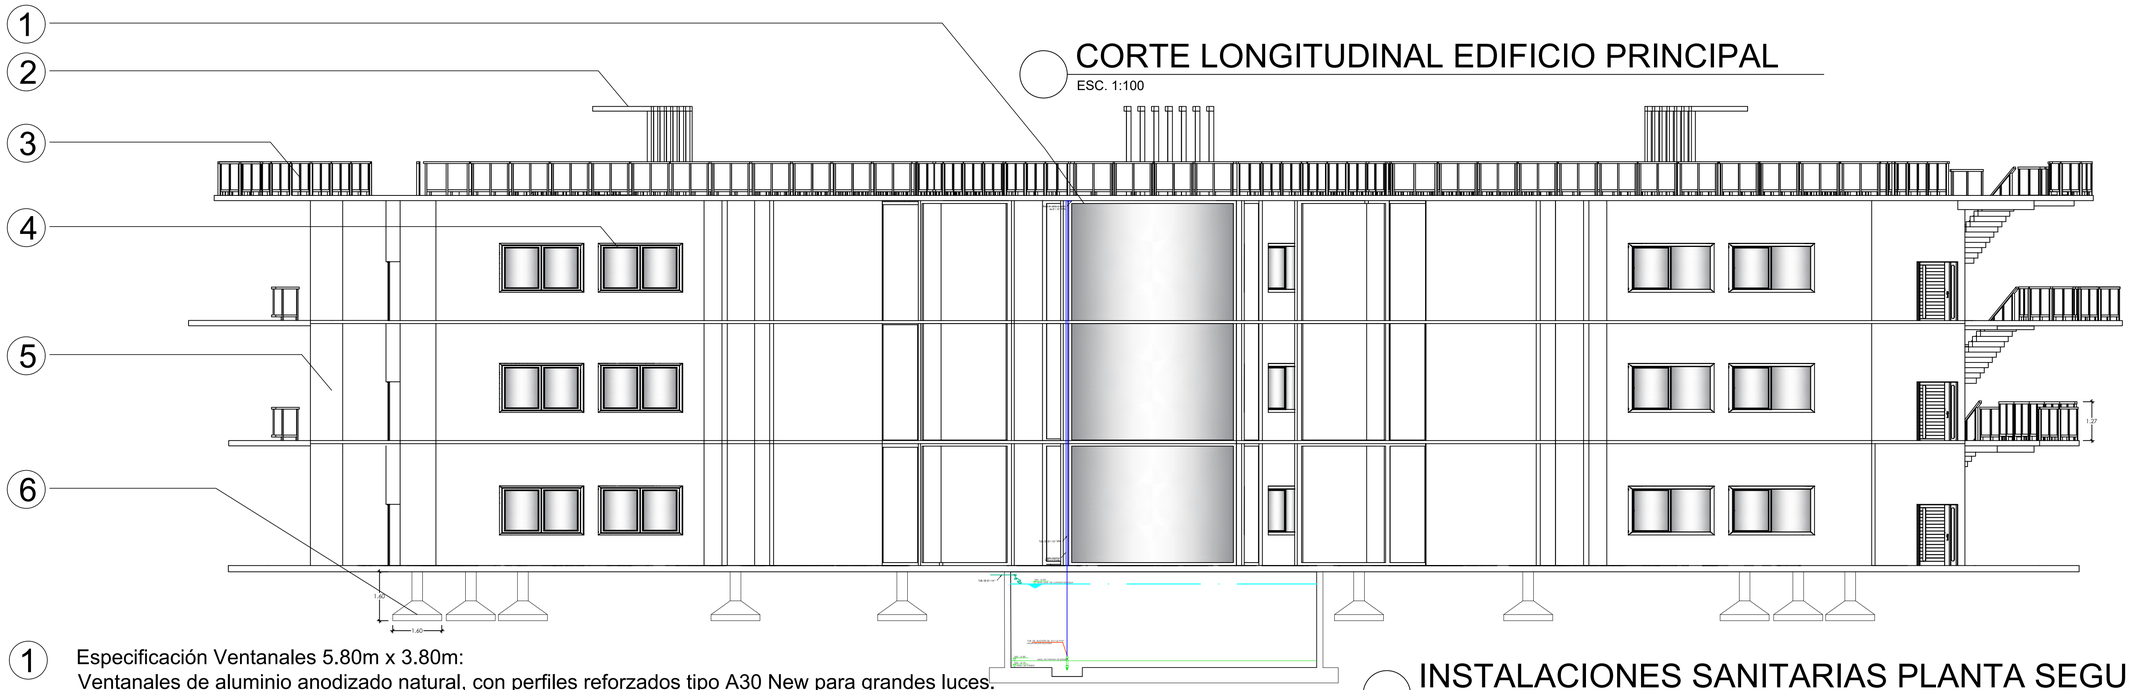

1 Especificación Ventanales 5.80m x 3.80m:
Ventanales de aluminio anodizado natural, con perfiles reforzados tipo A30 New para grandes luces.
Vidrio doble vidriado hermético
(DVH) 4+12+4 mm, compuesto por vidrio exterior laminado (4+4 mm) y vidrio interior templado, garantizando seguridad y aislamiento térmico/acústico. Herrajes de acero inoxidable con cierres multipunto. Sellado perimetral con juntas de EPDM y siliconaestructural resistente a la intemperie.

2 Pérgola Terraza Verde:
Pérgola de madera dura tratada para intemperie (lapacho) con acabado protector tipo barniz marino.Estructura de 2.85 m de alto, con columnas laminadas de 15x15 cm, ancladas a la losa mediante zapatas metálicas galvanizadas y fijación química al hormigón. Vigas principales de 10x20 cm y vigas secundarias de 5x15 cm, dispuestas cada 50 cm. Cubierta con enrejado de listones de 5x5 cm, preparada para vegetación trepadora y sistema de riego. Uniones con tornillos de acero inoxidable y escuadras metálicas ocultas, selladas con silicona neutra. Estructura diseñada para soportar carga vegetal y alta humedad en clima subtropical.

3 Baranda de aluminio anodizado, con soportes cada 1.20 m y vidrio laminado 5+5 mm, fijado con herrajes tipo U y silicona estructural. Altura de 1.30m desde el piso, anclada a la losa con tacos químicos y pernos expansivos de acero inoxidable. Pasamanos continuo de aluminio, con uniones ocultas en esquinas y encuentros. Diseñada para resistir cargas de viento y uso en exteriores con alta humedad.


4 Ventanas de aluminio anodizado, con perfiles tipo A30 New. Vidrio doble vidriado hermético (DVH) 4+12+4 mm, compuesto por vidrio exterior laminado (4+4 mm) y vidrio interior templado, para seguridad y aislamiento térmico/acústico. Herrajes de acero inoxidable con cierres multipunto. Sellado perimetral con juntas de EPDM y silicona estructural resistente a la intemperie. Anclaje mediante tacos químicos y fijación oculta al marco estructural.

5 Revestimiento de laja natural en placas irregulares, instalado con adhesivo cementicio flexible apto para exteriores. Anclaje adicional mediante fijaciones mecánicas ocultas en zonas de mayor exposición. Sellado de juntas con mortero impermeable para evitar filtraciones. Tratamiento final con impermeabilizante transparente para protección contra humedad y hongos.

6 Fundación mediante zapatas aisladas de 1.60 m x 1.60 m, armadas con acero de refuerzo longitudinal y estribos perimetrales. Las zapatas se vinculan a las columnas mediante pedestales de hormigón armado. Hormigón de resistencia H25, con asentamiento adecuado para garantizar la estabilidad de la estructura que soporta 3 pisos más una terraza. La base se apoya sobre terreno compactado y nivelado, con capa de limpieza de hormigón pobre (H8). Impermeabilización en los bordes para evitar la absorción de humedad del subsuelo.

INSTALACIONES SANITARIAS PLANTA SEGUNDO PISO

ESC. 1:100

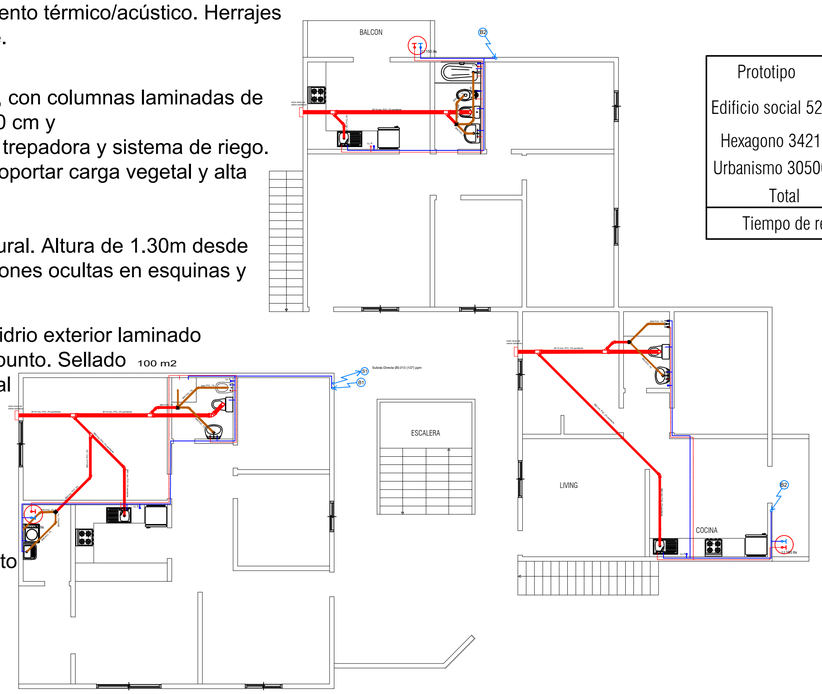

Prototipo	Presupuesto
Edificio social 525 m2	638.925.000ARS
Hexagono 3421 m2	4.163.357.000ARS
Urbanismo 30500 m2	27.450.000.000ARS
Total	32.252.282.000ARS
Tiempo de realización 3 a 6 años	

Escuela Provincial Educación Técnica N°4 O.E.A		Materia: Proyecto IV	6 Año A Maestro Mayor de Obra	**Proyecto: Edificios sociales e intervención urbana, Andres Gaspar Giai**
Profesor Asesor: Gustavo Yanssen		Equipo de Proyecto:	Amarilla Carlos, Antunez Gonzalo, Barrios Alan y Beling Alexander	Titulo lamina: Corte longitudinal e instalación Sanitaria
Fecha de inicio: 8/10/24	Fecha de finalización: 13/11/24	Fecha de presentación al publico: 14/11/24	Fecha de relevamiento: 1/10/24	Numero lamina: 7